



전남대학교병원
CHONNAM UNIVERSITY HOSPITAL

설계명 PROJECT TITLE

실

경

책임기술자

특기사항 NOTE

수정번호	수정내용	DATE	수정자	확인자	승인자
REV.					

도면명 DRAWING TITLE

제1층 1층 평면도

일 자 DATE 축 척 SCALE

2015 02 A1: 1/150
A3: 1/300

파일명 FILE NAME

도면번호 DRAWING NO.

A01-003

일련번호 SHEET NO.

□□□-□□□

1. 벽체 부호

DW15 : THK15 석고보드 2장+
C-90 W/24K 유리면 50T+
THK15 석고보드 2장

DW15W : THK15 석고보드 2장+
C-90 W/24K 유리면 50T+
THK15 방수석고보드+
THK15 CRC보드

DW15WW : THK15 CRC보드+
THK15 석고보드+
C-90 W/24K 유리면 50T+
THK15 방수석고보드+
THK15 CRC보드

DW20 : THK15 석고보드 2장+
C-50 W/24K 유리면 50T+
THK40 공간+ C-10T+
THK15 석고보드 2장

DW20W : THK15 석고보드 2장+
C-50 W/24K 유리면 50T+
THK40 공간+ C-50T+
THK15 방수석고보드+
THK15 CRC보드

DW11.5W : THK12.5 석고보드 2장+
C-65 W/24K 유리면 60T+
THK12.5 방수석고보드+
THK12.5 CRC보드

DW11.5WW : THK12.5 CRC보드+
THK12.5 방수석고보드+
C-65 W/24K 유리면 60T+
THK12.5 방수석고보드+
THK12.5 CRC보드

DW11.5W : THK12.5 석고보드 2장+
C-65 W/24K 유리면 50T+
THK12.5 방수석고보드+
THK12.5 CRC보드

DW11 : THK12.5 석고보드 2장+
C-65 W/24K 유리면 60T

BR1 : 1.08 시멘트벽돌 쌓기
BR5 : 0.98 시멘트벽돌 쌓기
BL8 : 8" 보강블럭 쌓기

*화장실 세면기는 건축기준,
화장실 세면기 상판은 인조대리석, 하부장상판
거울은 전면거울 기준
큐비클 H=2,200(LG 레스트돌 R-700)

H=800 HANDRAIL: Ø38 SUS HAIRLINE FINISH
경사로: 1950X80T 화장석 천더들

건축선
EL±0
두껍서: 400X100T 화장석 붙이기

기준 건물
중축부분

○ 렌스
○ 전화선
○ 콘센트(기본2구)
○ 세면대
○ 싱크대
○ TV
○ GIGA
○ 장수기
○ O. SUCTION
○ 대들
○ 창수상기
○ 오물처리대
○ PDP
○ ART WALL(SPACE WALL)

상부 캐노피 골선
기준 지하층 외벽선

환기탑

상부 캐노피 골선

기준 지하층 외벽선

환기탑

상부 캐노피 골선

기준 지하층 외벽선

환기탑

상부 캐노피 골선

기준 지하층 외벽선

환기탑

상부 캐노피 골선

기준 지하층 외벽선



전남대학교병원
CHONNAM UNIVERSITY HOSPITAL

설계명 PROJECT TITLE

설 계

검 토

책임기술자

특기사항 NOTE

설계변경 DESCRIPTION OF REV.	일 자 DATE	작성 DRAW	검 토 CHECK	승 인 APPR
--------------------------------	-------------	------------	--------------	-------------

협 의

도면명 DRAWING TITLE

제1동 2층 평면도

일 자 DATE	축척 SCALE
-------------	-------------

2015 02	A1 : 1/150 A3 : 1/300
---------	--------------------------


파일명 FILE NAME

도면번호 DRAWING NO.

A	0	1	-	0	0	4
---	---	---	---	---	---	---

일련번호 SHEET NO.

□	□	□	-	□	□	□	□
---	---	---	---	---	---	---	---

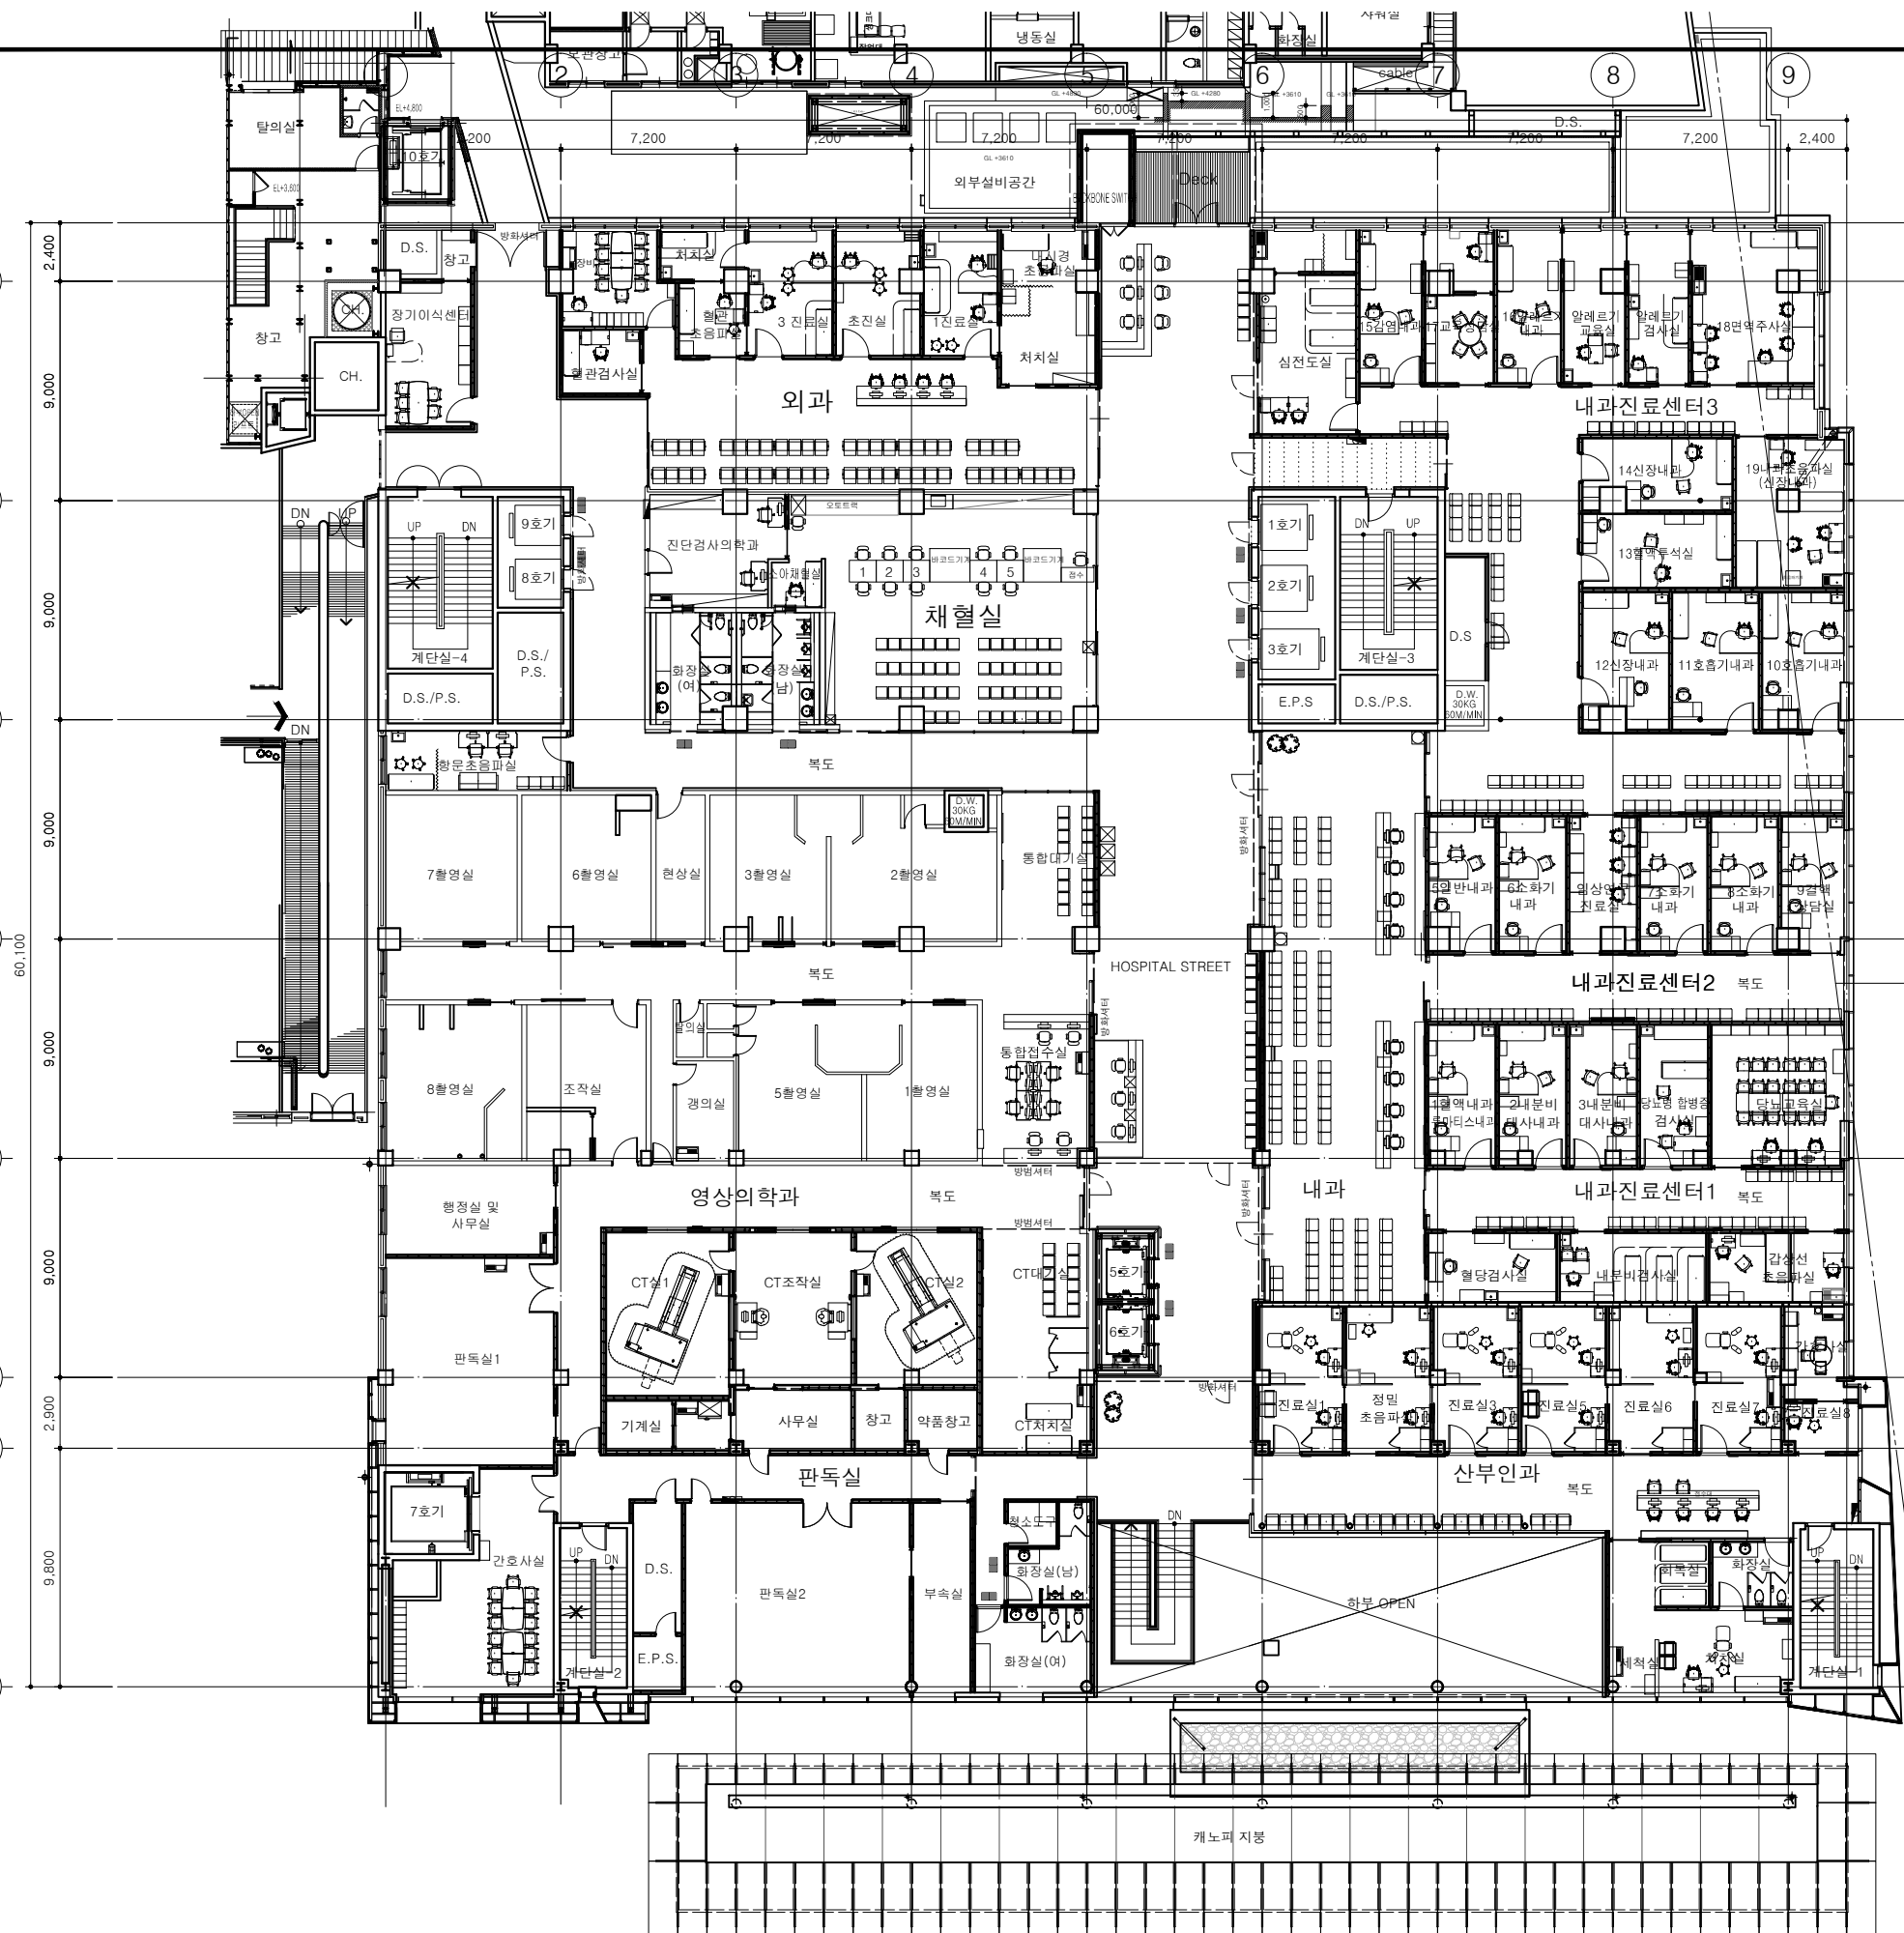

대지안의공지
3M 후퇴선

기존건물
↑
↓
증축부분

1 2층 평면도
축척 : A1: 1/150
A3: 1/300
면적=3,652.73m2