



2주차장 1층

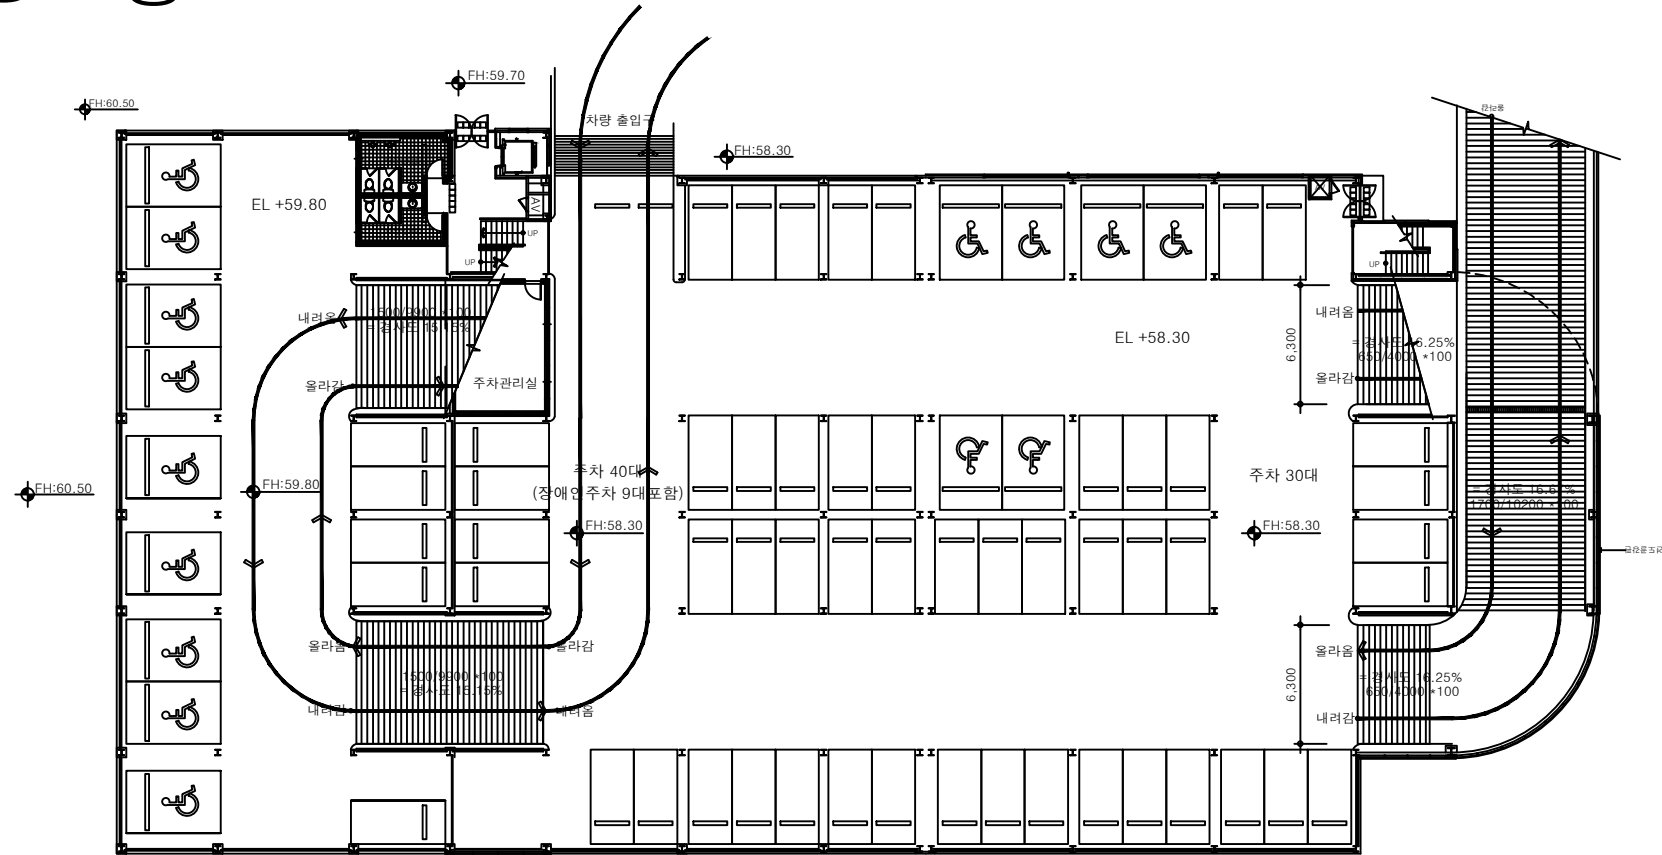

1층 평면도(기준)
SCALE A1 : 1/200
A3 : 1/400

2주차장 2층

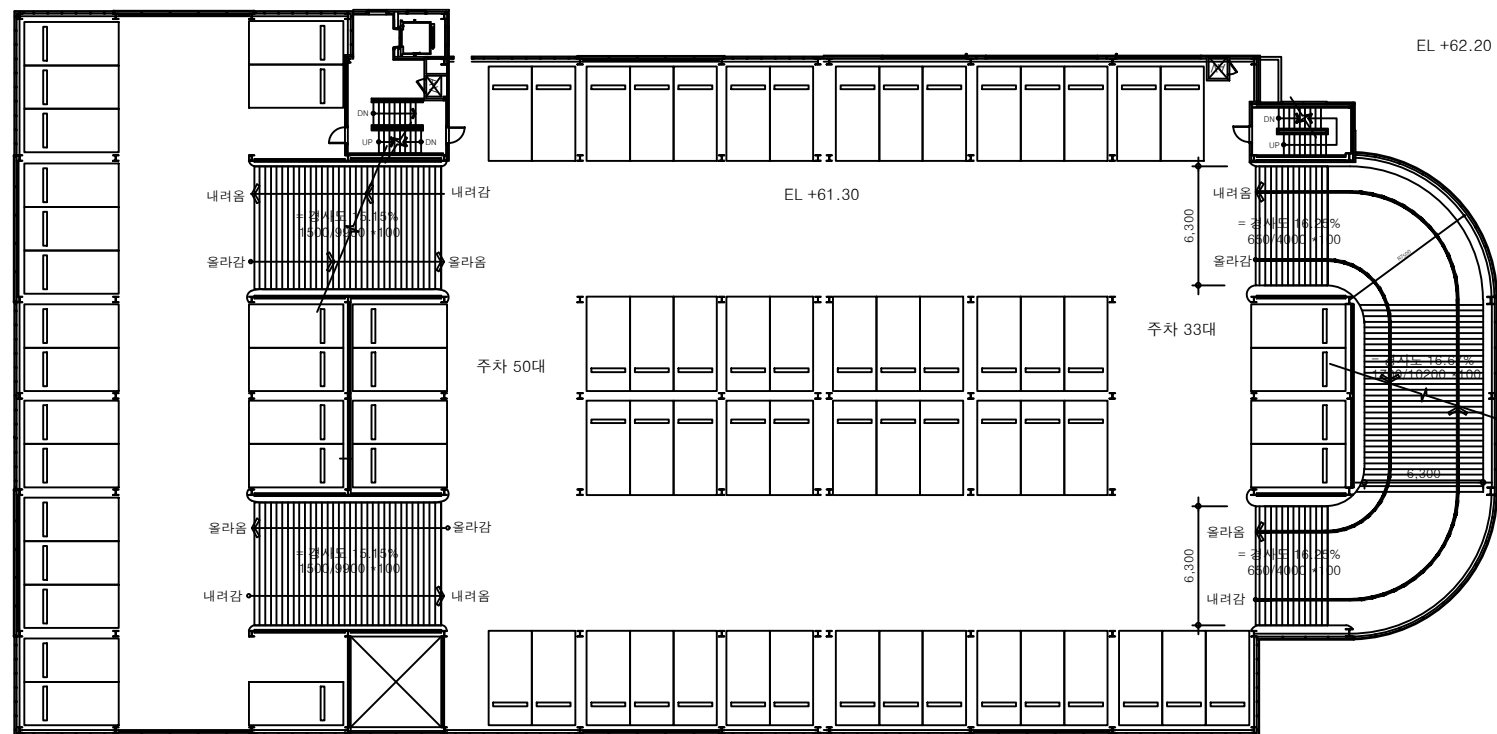

2층 평면도(기준)
SCALE A1 : 1/200
A3 : 1/400



전남대학교병원

설계명 PROJECT TITLE

의생명연구 지원센터 부대시설
설계용역

주 기 NOTES

- *전층 주차야하드너시공
- *전층 CAR STOPPER 철거후 재설치
- *전층 주차선 마크작업 추가
- *1-7층 낙엽방지 그물망설치
- *전층선홍통 철거후 신설
- *전층 추락방지시설 설치

수 정 REVISION

△		
△		
△		
△		
△		
△		

설 계 DRAWN BY

검 토 CHECKED BY

심 사 REVIEWED BY

제 출 SUBMITTED BY

일 자 DATE

2013.12.

도 면 명 SUBJECT TITLE


1, 2층 평면도(기준)

도면번호 DRAWING NO

A12-001


Architects EL and JAGYUNGIE Design group
www.elandjagyungie.com
(주) 건축사사무소 이엘앤드자영제 디자인그룹

2주차장 3층

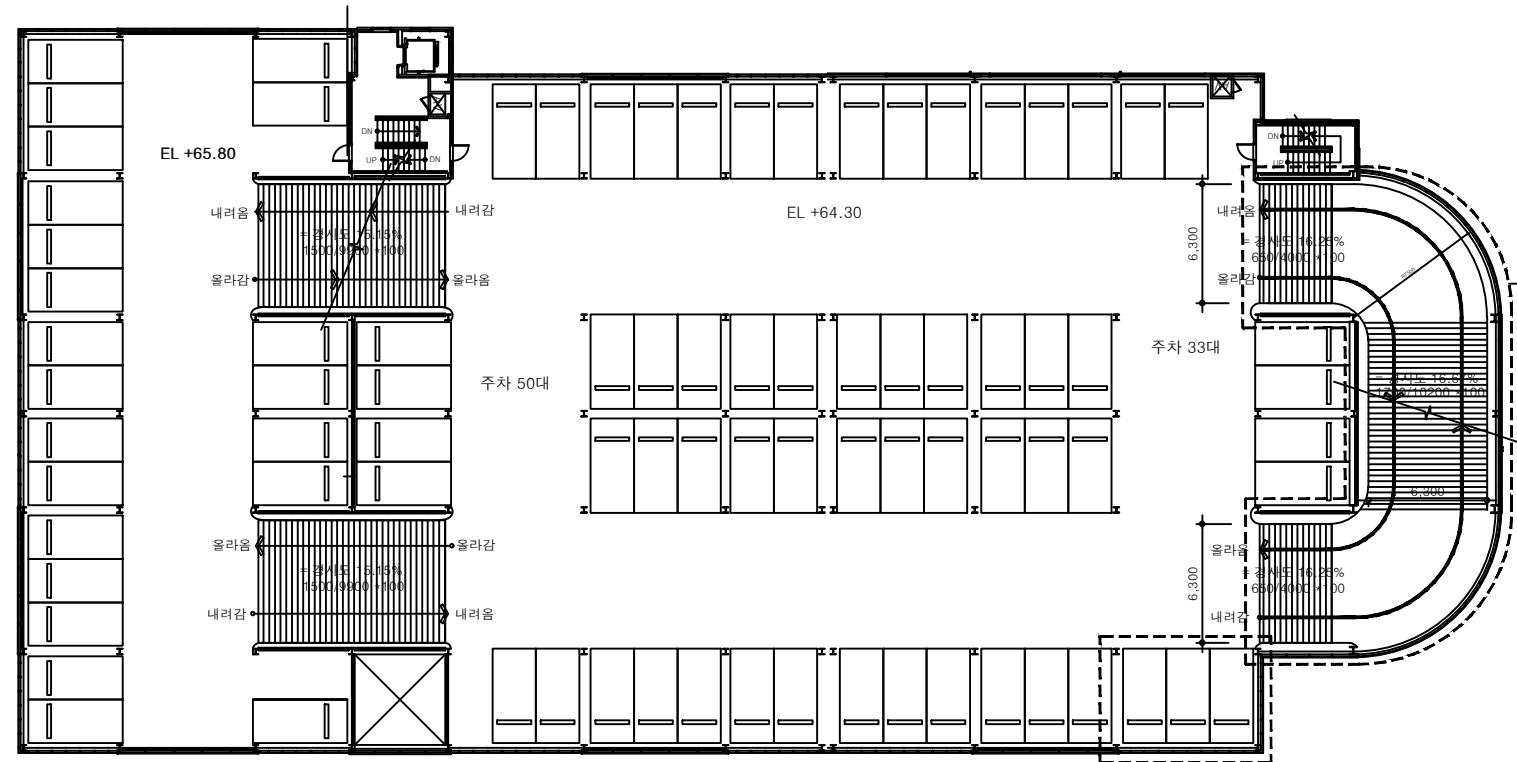

3층 평면도(기존)
SCALE A1 : 1/200
A3 : 1/400

2주차장 4층

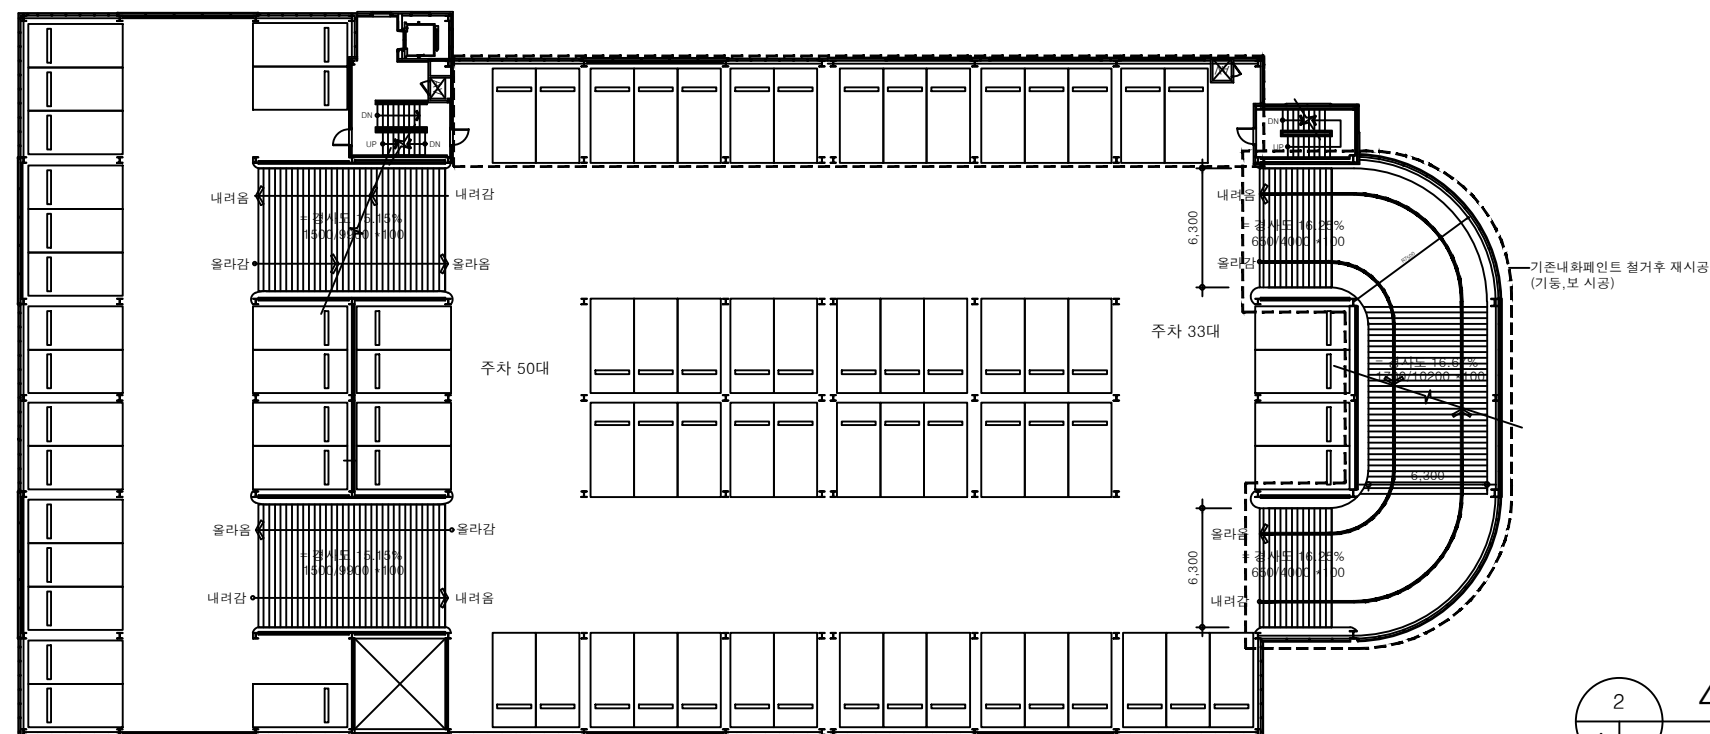

4층 평면도(기존)
SCALE A1 : 1/200
A3 : 1/400



전남대학교병원

설계명 PROJECT TITLE

의생명연구 지원센터 부대시설
설계용역

주 기 NOTES

- *전층 후로아하드너시공
- *전층 CAR STOPPER 철거후 재설치
- *전층 주차선 마크작업 추가
- *1-7층 낙엽방지 그물망설치
- *전층선홀통 철거후 신설

□ 램프상부보 내화페인트추가 (표기부분추가)

*전층 추락방지시설 설치

수 정 REVISION

△		
△		
△		
△		
△		

설 계 DRAWN BY

검 토 CHECKED BY

심 사 REVIEWED BY

제 출 SUBMITTED BY

일 자 DATE

2013.12.


도 면 명 SUBJECT TITLE

3, 4층 평면도(기존)

도면번호 DRAWING NO


A12-002

2주차장 5층

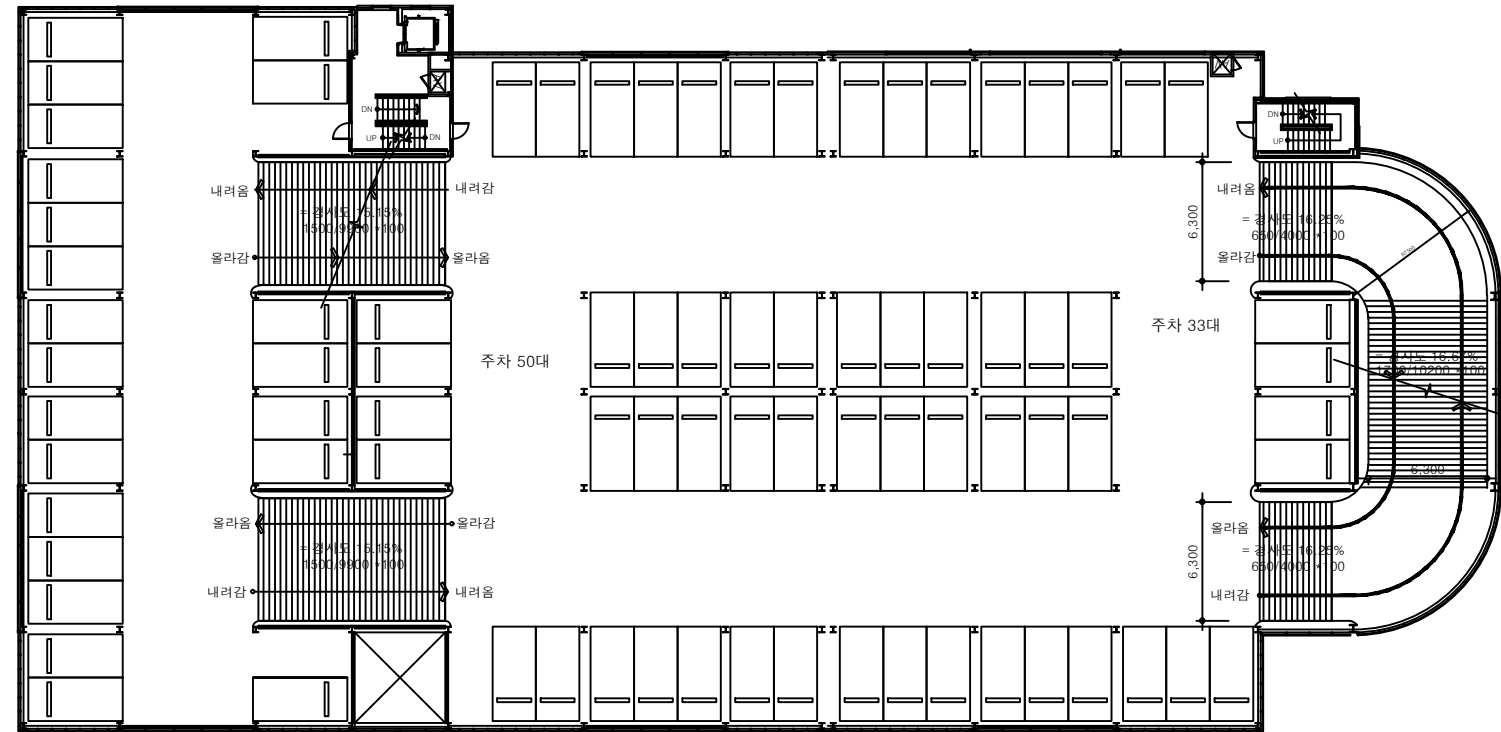

5층 평면도
SCALE A1 : 1/200
A3 : 1/400

2주차장 6층

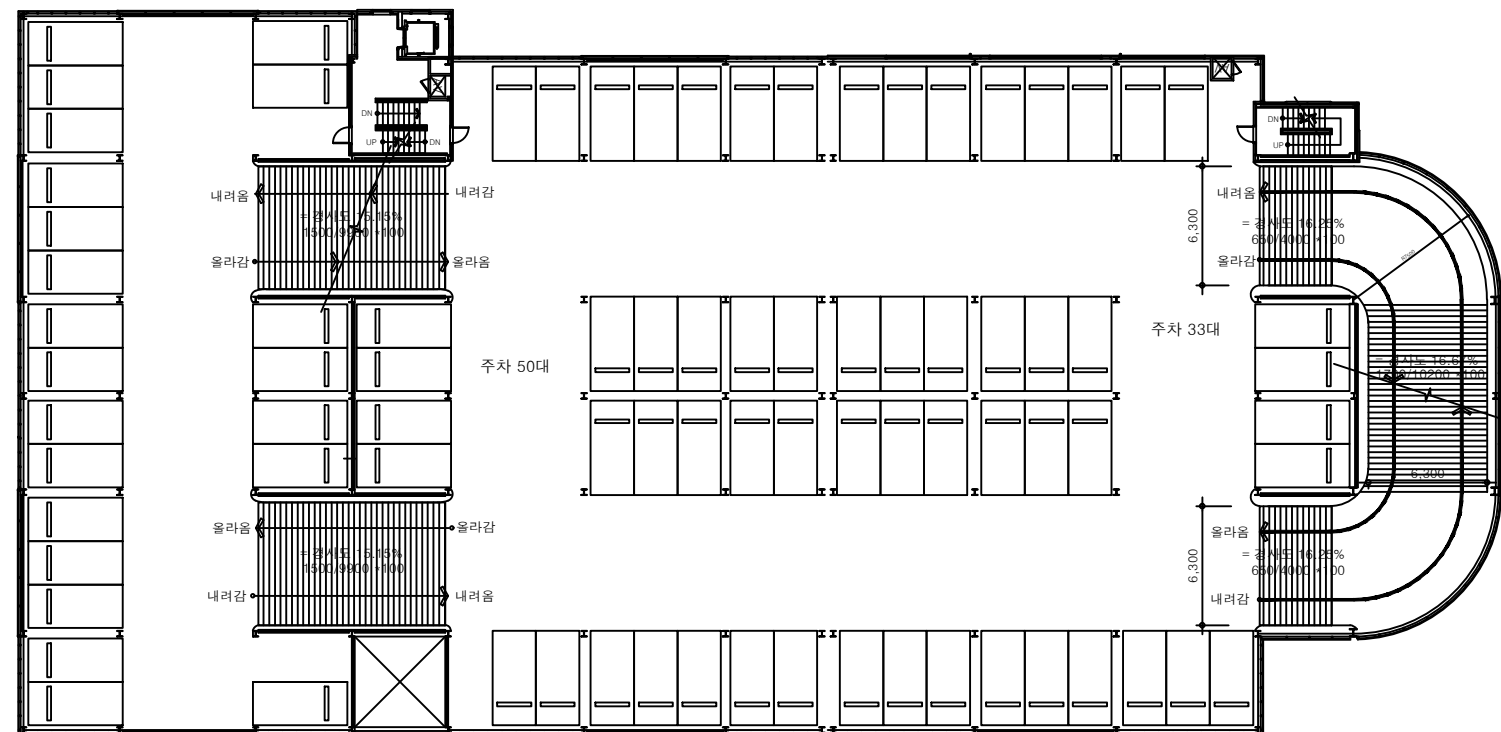

6층 평면도(신설)
SCALE A1 : 1/200
A3 : 1/400



전남대학교병원

설계명 PROJECT TITLE

의생명연구 지원센터 부대시설
설계용역

주 기 NOTES

- *전층 주차야하드너시공
- *전층 CAR STOPPER 철거후 재설치
- *전층 주차선 마크작업 추가
- *1-7층 낙엽방지 그물망설치
- *전층선홀통 철거후 신설

□ 램프상부보 내화페인트추가 (표기부분추가)

*전층 추락방지시설 설치

수 정 REVISION

△		
△		
△		
△		
△		

설 계 DRAWN BY

검 토 CHECKED BY

심 사 REVIEWED BY

제 출 SUBMITTED BY

일 자 DATE

2013.12.

도 면 명 SUBJECT TITLE



5층(기존), 6층(증축) 평면도

도면번호 DRAWING NO

A12-003

Architects E&L and JAGYUNGIE Design group
www.eandj.com 02-384-4435 Fax 02-384-4432
(주) 건축사사무소 이엘앤드자영제 디자인그룹



2주차장 7층

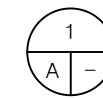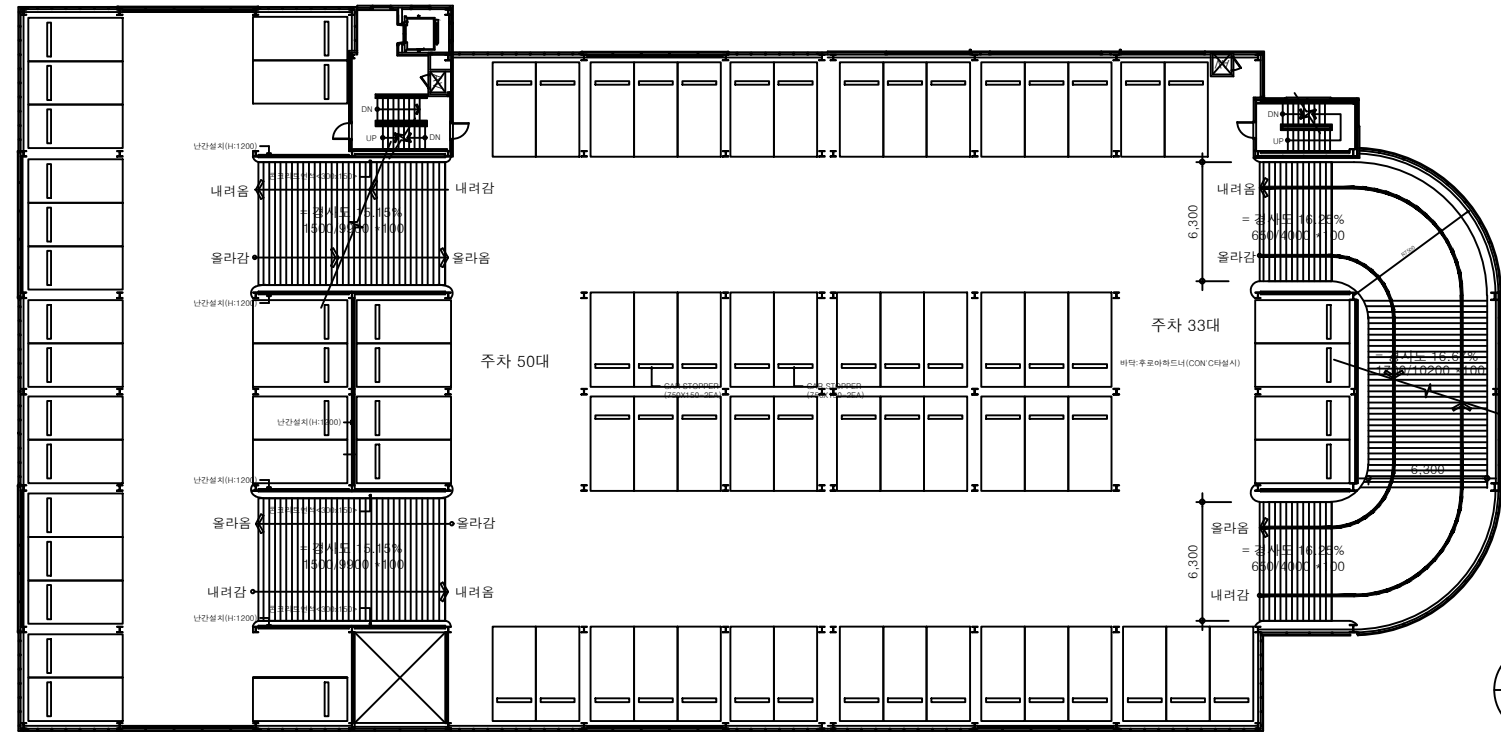

7층 평면도(신설)

SCALE A1 : 1/200
A3 : 1/400

2주차장 옥상층

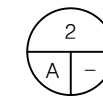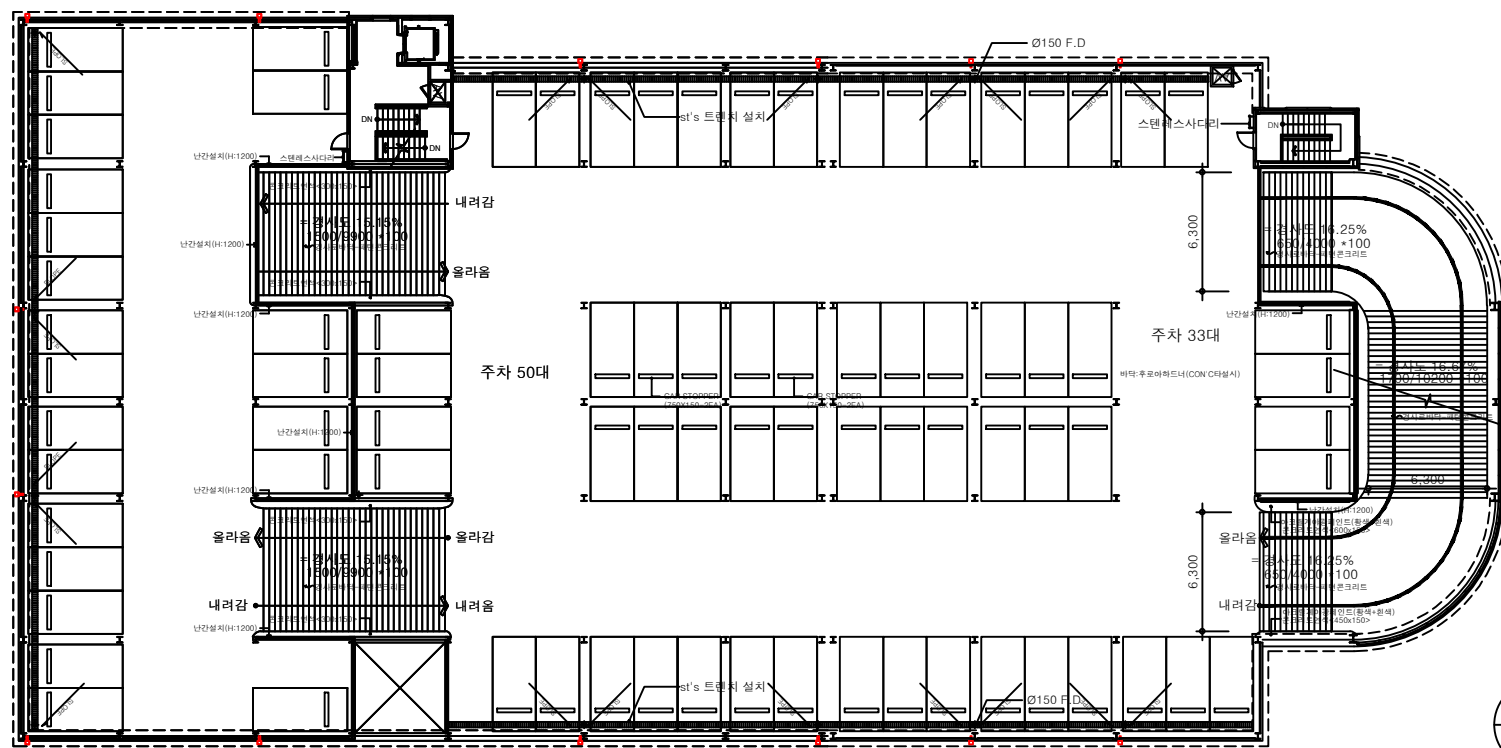

옥상 평면도(신설)

SCALE A1 : 1/200
A3 : 1/400



전남대학교병원

설계명 PROJECT TITLE

의생명연구 지원센터 부대시설
설계용역

주 기 NOTES

- *전층 주차야하드너시공
- *전층 CAR STOPPER 철거후 재설치
- *전층 주차선 마크작업 추가
- *1-7층 낙엽방지 그물망설치
- *전층선홀통 철거후 신설

□ 램프상부보 내화페인트추가 (표기부분추가)

*전층 추락방지시설 설치

수 정 REVISION

△		
△		
△		
△		
△		

설 계 DRAWN BY

검 토 CHECKED BY

심 사 REVIEWED BY

제 출 SUBMITTED BY

일 자 DATE

2013.12.

도 면 명 SUBJECT TITLE

7층, 지붕 평면도(증축)

도면번호 DRAWING NO

A12-004

Architects EL and JAGYUNGJIE Design group
www.elandjagye.com TEL 010-4300-4430 FAX 010-4300-4431
(주) 건축사사무소 이엘앤드자영제 디자인그룹