


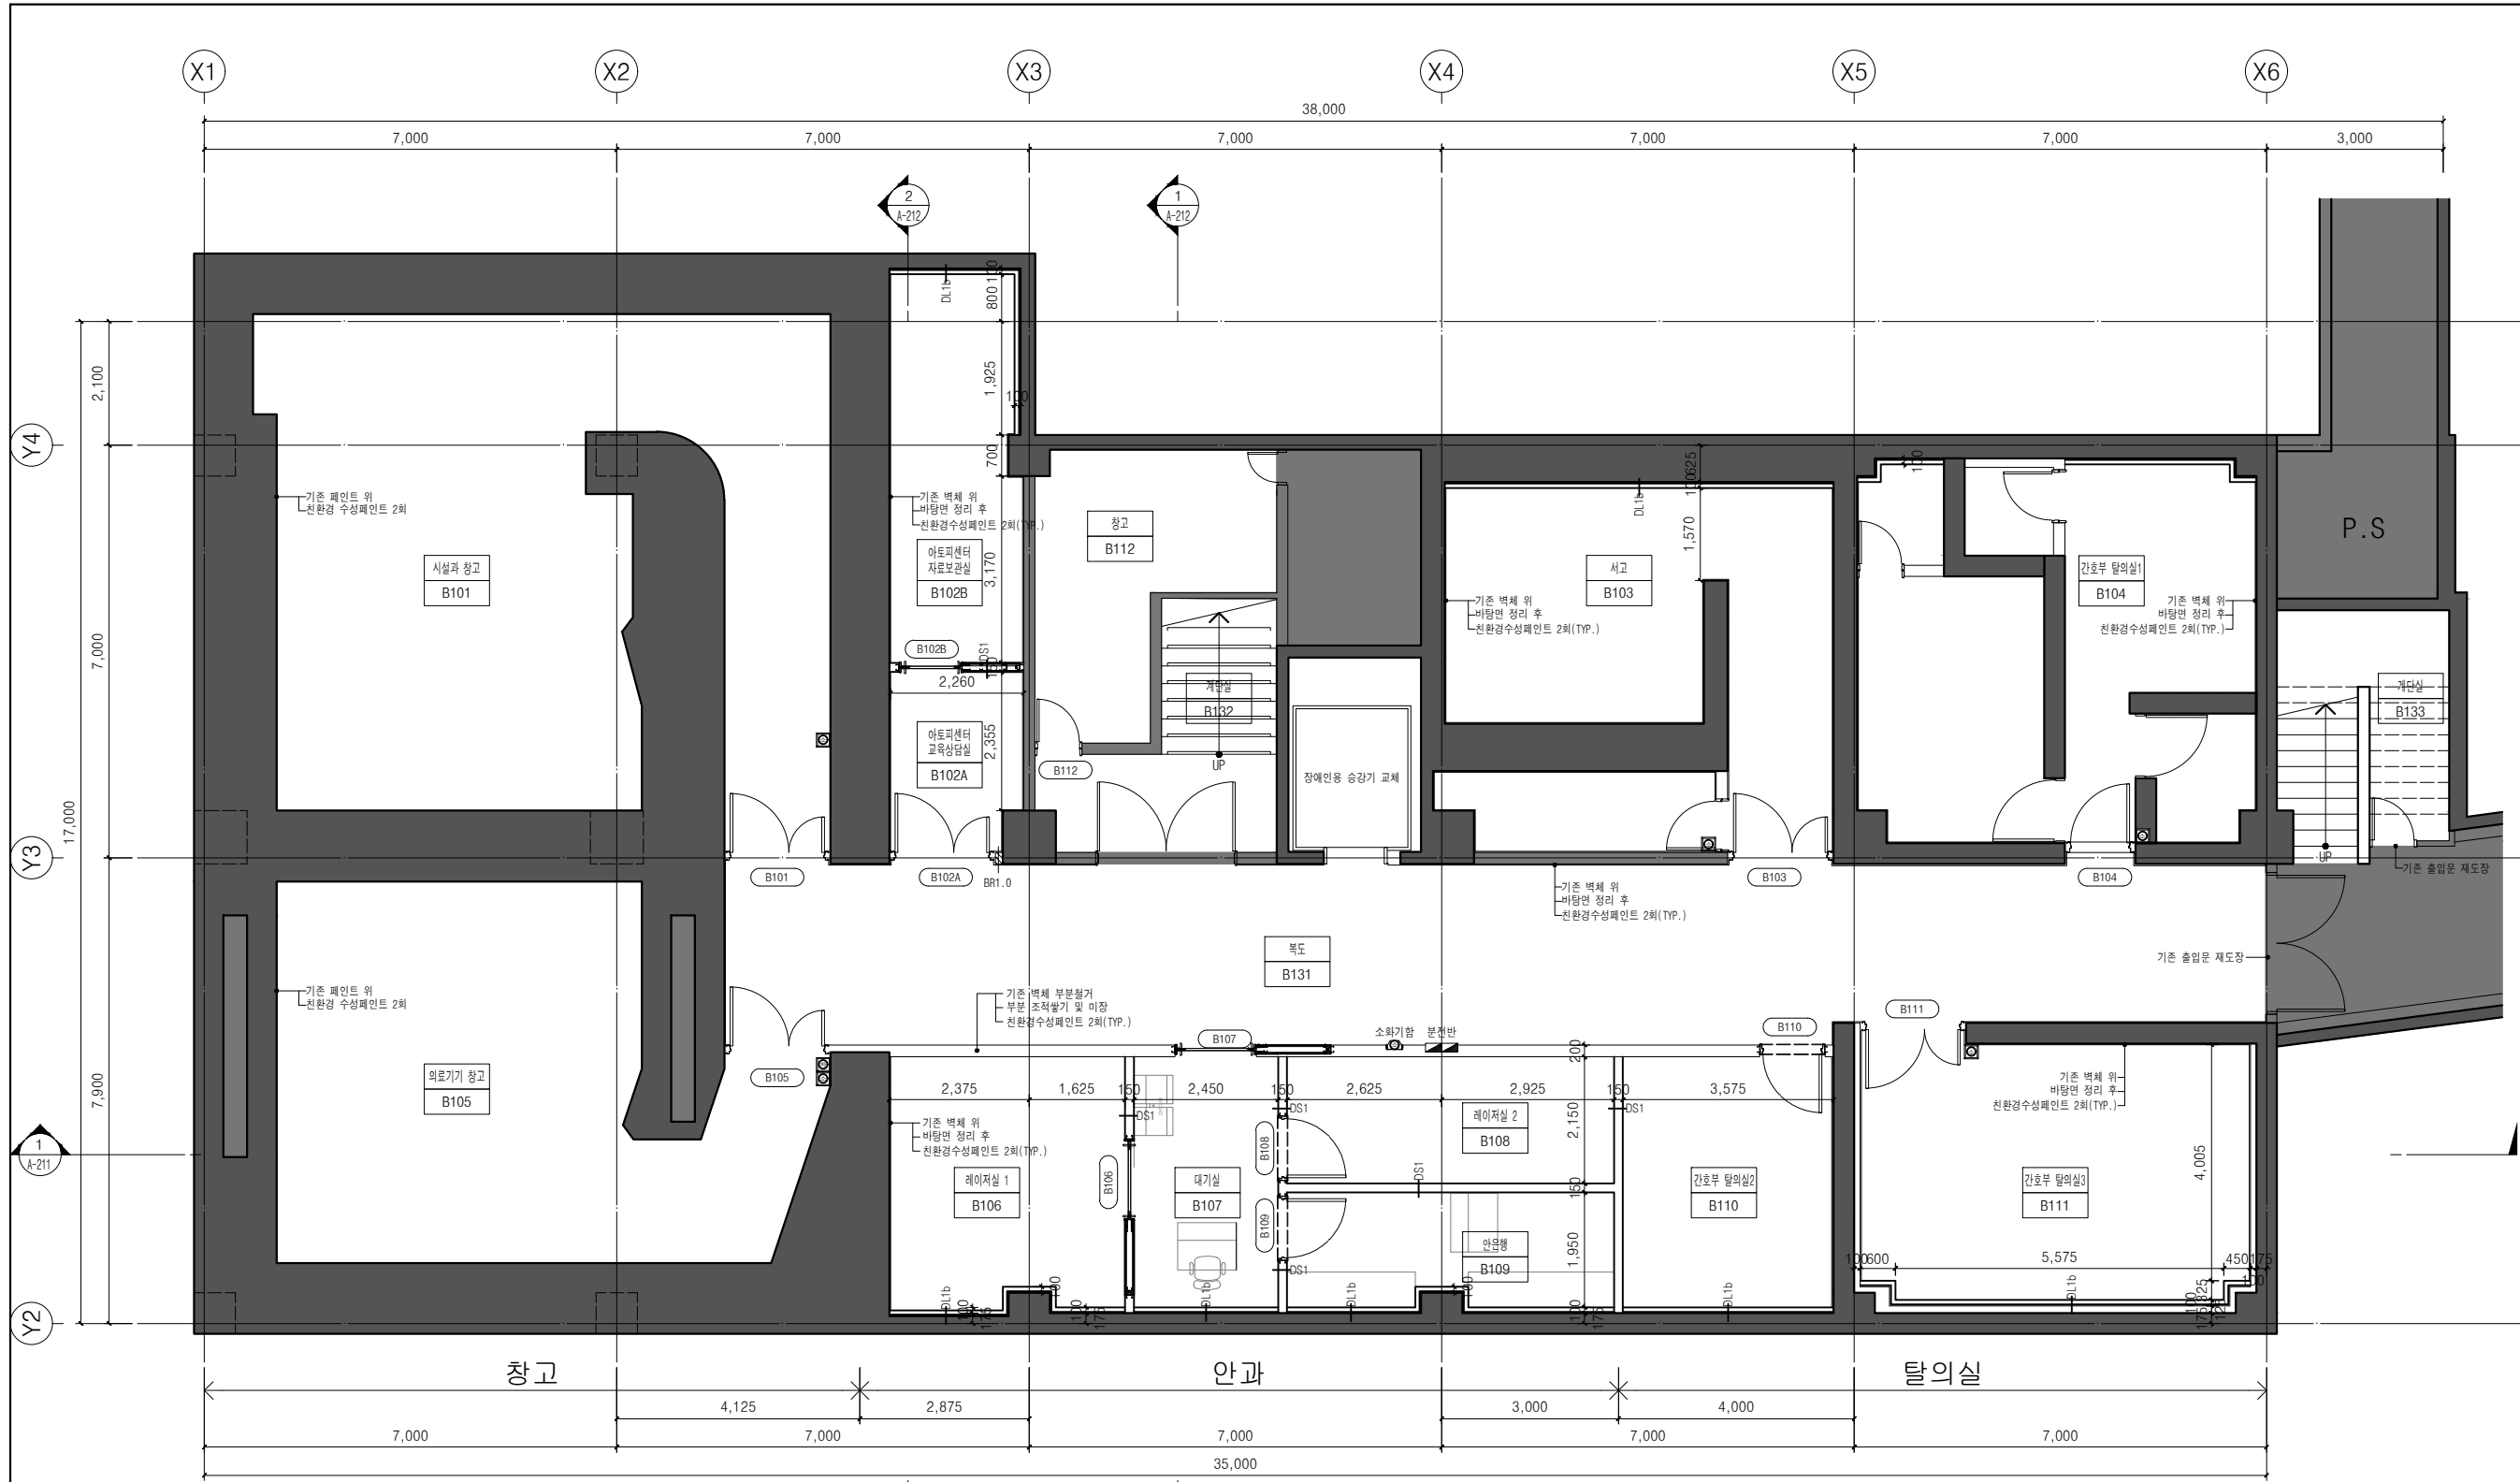

- NOTE
- 벽체무호
BL6 : 6" 보강블럭쌓기
BR0.5 : 0.5B 시멘트벽돌쌓기
BR0.75 : 0.75B 시멘트벽돌쌓기
BR1.0 : 1.0B 시멘트벽돌쌓기
석고보드 : 석고보드 계획도와 상세도 참조
분전반 : 전기공사 전력간선 평면도 참조
 - 전남대학교 3동 리모델링 공사는 골조공사를 제외하며 범위는 지하1층~지상9층까지임.
아래 범위에 면하는 벽체를 철거하지 않는 원칙으로 하며, 평면도에 부호가 표기된 벽체만 신설 벽체임.
단, 승강기 교체는 공사범위에 포함함.
= 공사범위 제외
= 환경개선범위(벽체유지, 마감재시공)
= 부분 공사범위 제외(천장만 교체)
= 인테리어 공사
 - 계단실과 EL 홀은 "환경개선" 대상이며, 실내재로 마감표 기준으로 공사항.
 - 전남대학교병원 3동 주변의 포장 및 조경은 신설 개도피 및 실외기에 간섭되는 구간에 한해서 철거 후 재시공함.
 - 출입문, 하드웨어, 석고보드 벽체, CONC' BLOCK, 조적 벽체는 모두 건축 공사분임.
단, 벽체의 마감과 천장재, 천장틀, 바닥 마감은 인테리어 공사
 - 기존 방화구획과 그에 해당하는 벽체 공사범위 제외이며, 방화문은 재도색만 할 것
 - 승강기 교체는 본 공사에 포함함.
 - 기존 설비공간의 점검문은 존치 및 페인트 재시공 할 것.
 - 가구는 모두 공사범위 제외임. 단, 상세도가 있는 붙박이장과 인테리어 공사에 포함된 가구는 포함함.
 - 본 공사에 엘리베이터 1대 교체 포함함
 - 소화전과 소화기는 매입형으로 설치 할 것. (A-803_잡상세도.DWG 참조 할 것.)
 - 지상1층 영상의학과 대기공간 공사범위는 확장될 수 있으며, 감독관과 협의하여 SHOP DWG 작성 후 시공할 것.
 - 샤프트 내부는 에폭시프라이머로 6면 시공 및 오픈구간 방화실로 메울것.
 - 소화기함, 분전반의 위치는 건축도면 기준으로 시공 할 것.
 - 벽체 설치시 분전반 크기를 고려하여 조정 후 감독관의 승인을 득할 것.

NO.	DATE	REVISIONS	DRWG.	APPRV.
-----	------	-----------	-------	--------




SAC INTERNATIONAL LTD.
ARCHITECTS-CONSULTANTS
서울특별시 강남구 테헤란로 152 동원빌딩 11층 주식회사 서울건축

PROJECT TITLE
전남대학교병원
제3동 진료공간 재배치 건축공사

DRAWING TITLE
지하1층 평면도

APPROVAL	이민화	PROJECT NO.	21043
CHECK	이승우	FILE NAME	A-101.DWG
DRAWING	이현지	DRAWING NO.	
SCALE	A1: 1/60 A3: 1/120		
DATE	2022.6.		A-101

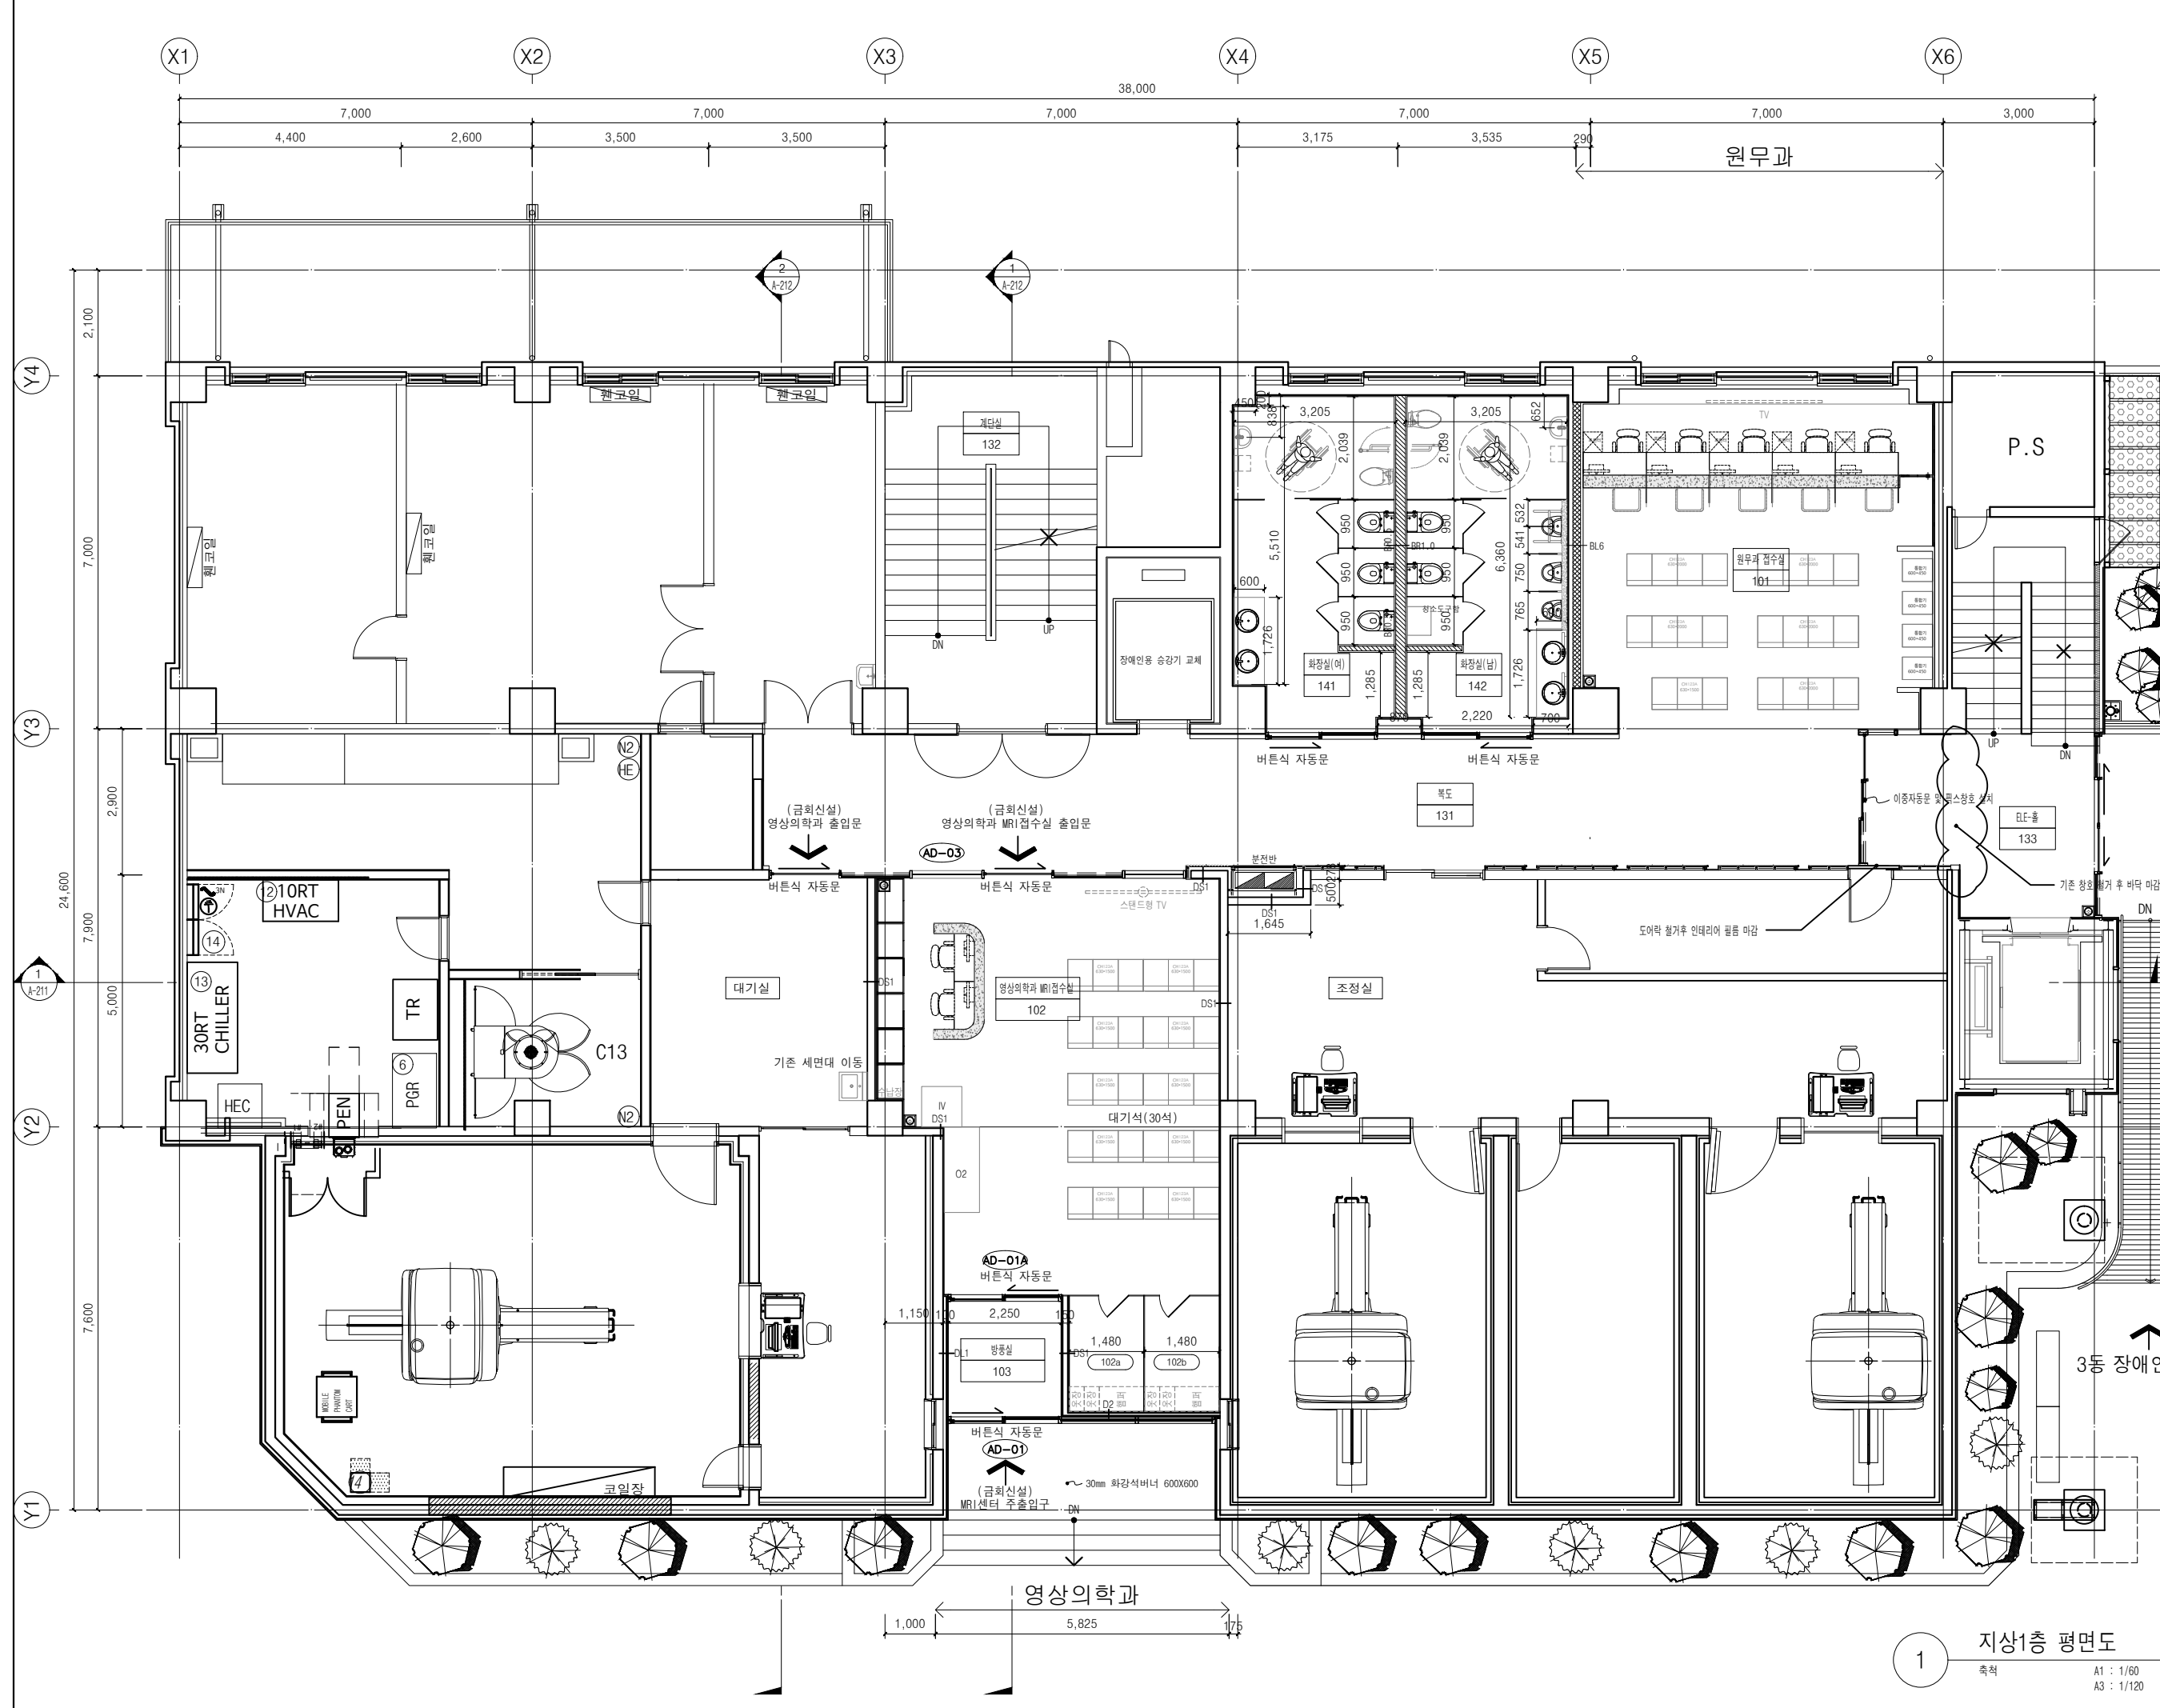

NOTE

- 벽체무호
BL6 : 6" 보강블럭쌓기
BR0.5 : 0.5B 시멘트벽돌쌓기
BR0.75 : 0.75B 시멘트벽돌쌓기
BR1.0 : 1.0B 시멘트벽돌쌓기
석고보드 : 석고보드 계획도와 상세도 참조
분전반 : 전기공사 전력간선 평면도 참조
- 전남대학교 3동 리모델링 공사는 골조공사를 제외하며 범위는 지하1층~지상9층까지임.
아래 범위에 면하는 벽체를 철거하지 않는 원칙으로 하며, 평면도에 부호가 표기된 벽체만 신설 벽체임.
단, 승강기 교체는 공사범위에 포함함.
= 공사범위 제외
= 환경개선범위(벽체유지, 마감재시공)
= 부분 공사범위 제외(천장만 교체)
= 인테리어 공사
- 계단실과 EL 홀은 "환경개선" 대상이며, 실내재료 마감표 기준으로 공사함.
- 전남대학교병원 3동 주변의 포장 및 조경은 신설 개도 및 실외기에 간섭되는 구간에 한해서 철거 후 재시공함.
- 출입문, 하드웨어, 석고보드 벽체, CONC' BLOCK, 조적 벽체는 모두 건축 공사분임.
단, 벽체의 마감과 천장재, 천장틀, 바닥 마감은 인테리어 공사
- 기존 방화구획과 그에 해당하는 벽체 공사범위 제외이며, 방화문은 재도색만 할 것
- 승강기 교체는 본 공사에 포함함.
- 기존 설비공간의 점검문은 존치 및 페인트 재시공 할 것.
- 가구는 모두 공사범위 제외임. 단, 상세도가 있는 물막이장과 인테리어 공사에 포함된 가구는 포함함.
- 본 공사에 엘리베이터 1대 교체 포함함
- 소화전과 소화기는 매입형으로 설치 할 것. (A-803_접상세도.DWG 참고 할 것.)
- 지상1층 영상의학과 대기공간 공사범위는 확충이 있으며, 감독관과 협의하여 900mm 작성 후 시공할 것.
- 바닥 내부에는 예폭프라이머로 6면 시공 및 200mm 방화살로 매울것.
- 조화기함, 분전반의 위치는 건축도면 기준으로 시공 할 것.
- 벽체 설치시 분전반 크기를 고려하여 조정 후 감독관의 승인을 득할 것.

DATE	REVISIONS	DRWG.	APPRV.

CHANG ARCHITECTURE
주식회사 종합건축사사무소 창

SAC INTERNATIONAL LTD.
ARCHITECTS-CONSULTANTS
서울특별시 강남구 테헤란로 12-1 11층 주식회사 서울건축

PROJECT TITLE
전남대학교병원
제3동 진료공간 재배치 건축공사

DRAWING TITLE
지상1층 평면도

APPROVAL	이민화	PROJECT NO.	21043
CHECK	이승우	FILE NAME	A-102.DWG
DRAWING	이현지	DRAWING NO.	A-102
SCALE	A1 : 1/60 A3 : 1/120		
DATE	2022.6.		

- NOTE
- 벽체무호
BL6 : 6" 보강블럭쌓기
BR0.5 : 0.5B 시멘트벽돌쌓기
BR0.75 : 0.75B 시멘트벽돌쌓기
BR1.0 : 1.0B 시멘트벽돌쌓기
석고보드: 석고보드 계획도와 상세도 참조
분전반: 전기공사 전력간선 평면도 참조
 - 전남대학교 3동 리모델링 공사는 골조공사를 제외하며 범위는 지하1층~지상9층까지임.
아래 범위에 면하는 벽체를 철거하지 않는 원칙으로 하며, 평면도에 부호가 표기된 벽체만 신설 벽체임.
단, 승강기 교체는 공사범위에 포함함.
 - 계단실과 EL 홀은 "환경개선" 대상이며, 실내재료 마감표 기준으로 공사함.
 - 전남대학교병원 3동 주변의 포장 및 조경은 신설 캐노피 및 실외기에 간섭되는 구간에 한해서 철거 후 재시공함.
 - 출입문, 하드웨어, 석고보드 벽체, CONC' BLOCK, 조적 벽체는 모두 건축 공사분임.
단, 벽체의 마감과 천장재, 천장틀, 바닥 마감은 인테리어 공사
 - 기존 방화구획과 그에 해당하는 벽체 공사범위 제외이며, 방화문은 재도색만 할 것
 - 승강기 교체는 본 공사에 포함함.
 - 기존 설비공간의 점검문은 손치 및 페인트 재시공 할 것.
 - 가구는 모두 공사범위 제외임. 단, 상세도가 있는 붙박이장과 인테리어 공사에 포함된 가구는 포함함.
 - 본 공사에 엘리베이터 1대 교체 포함함
 - 소화전과 소화기는 매입형으로 설치 할 것. (A-803_잡상세도.DWG 참조 할 것.)
 - 지상1층 영상의학과 대기공간 공사범위는 확장될 수 있으며, 감독관과 협의하여 SHOP DWG 작성 후 시공할 것.
 - 샤프트 내부는 에폭시프라이머로 6면 시공 및 오픈구간 방화실로 매울것.
 - 소화기함, 분전반의 위치는 건축도면 기준으로 시공 할 것.
 - 벽체 설치시 분전반 크기를 고려하여 조정 후 감독관의 승인을 득할 것.

NO.	DATE	REVISIONS	DRWG.	APPRV.
-----	------	-----------	-------	--------




INTERNATIONAL LTD.
TECTS & CONSULTANTS

주식회사 서울건축

전남대학교병원
료공간 재배치 건축공사

민화	PROJECT NO.	21043
승우	FILE NAME	
	DRAWING NO.	

1 지상2층 평면도
축척 A1 : 1/60 A3 : 1/120

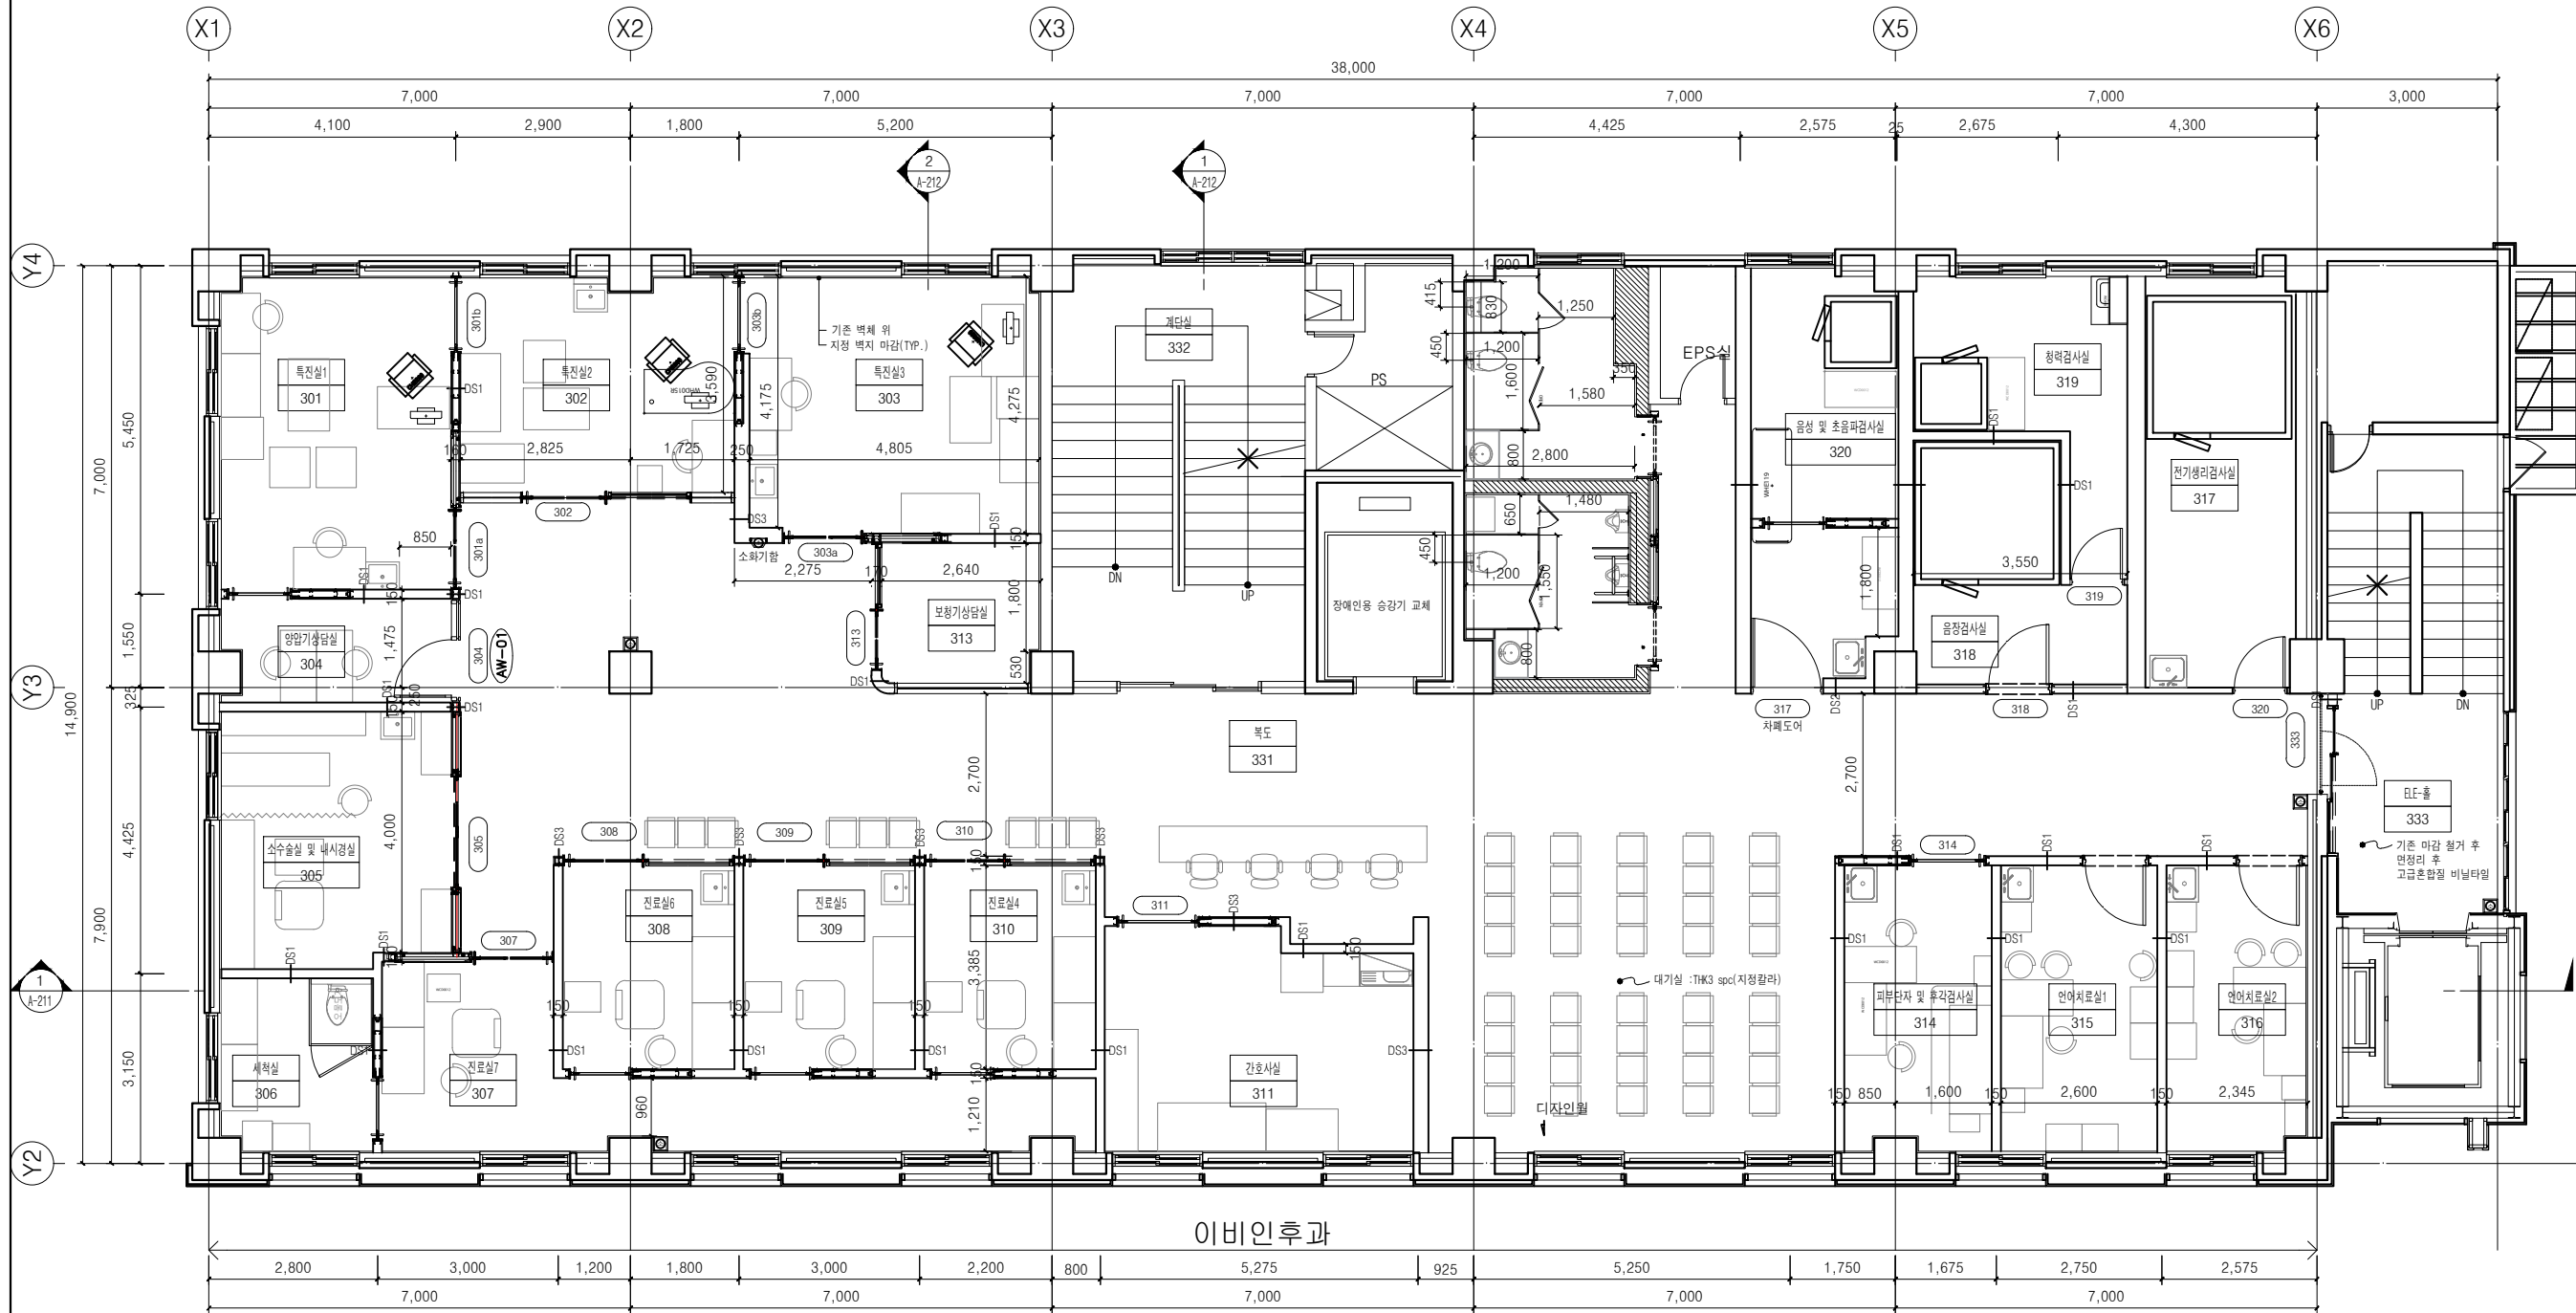

- NOTE
- 벽체무호
BL6 : 6" 보강블럭쌓기
BR0.5 : 0.5B 시멘트벽돌쌓기
BR0.75 : 0.75B 시멘트벽돌쌓기
BR1.0 : 1.0B 시멘트벽돌쌓기
석고보드 : 석고보드 계획도와 상세도 참조
분전반 : 전기공사 전력간선 평면도 참조
 - 전남대학교 3동 리모델링 공사는 골조공사를 제외하며 범위는 지하1층~지상9층까지임.
아래 범위에 면하는 벽체를 철거하지 않는 원칙으로 하며, 평면도에 부호가 표기된 벽체만 신설 벽체임.
단, 승강기 교체는 공사범위에 포함함.
= 공사범위 제외
= 환경개선범위(벽체유지, 마감재시공)
= 부분 공사범위 제외(천장만 교체)
= 인테리어 공사
 - 계단실과 EL 홀은 "환경개선" 대상이며, 실내재료 마감표 기준으로 공사함.
 - 전남대학교병원 3동 주변의 포장 및 조경은 신설 캐노피 및 실외기에 간섭되는 구간에 한해서 철거 후 재시공함.
 - 출입문, 하드웨어, 석고보드 벽체, CONC BLOCK, 조적 벽체는 모두 건축 공사분임.
단, 벽체의 마감과 천장재, 천장틀, 바닥 마감은 인테리어 공사
 - 기존 방화구획과 그에 해당하는 벽체 공사범위 제외이며, 방화문은 재도색만 할 것
 - 승강기 교체는 본 공사에 포함함.
 - 기존 설비공간의 점검문은 손치 및 페인트 재시공 할 것.
 - 기타 모든 공사범위 제외임. 단, 상세도가 있는 붙박이장과 인테리어 공사에 포함된 가구는 포함함.
 - 본 공사에 엘리베이터 1대 교체 포함함
 - 소화전과 소화기는 매입형으로 설치 할 것. (A-803, 잡상세도.DWG 참조 할 것.)
 - 지상1층 영상의학과 대기공간 공사범위는 확장될 수 있으며, 감독관과 협의하여 SHOP DWG 작성 후 시공할 것.
 - 샤프트 내부는 에폭시프라이머로 6면 시공 및 오픈구간 방화실로 메울것.
 - 조화기함, 분전반의 위치는 건축도면 기준으로 시공 할 것.
벽체 설치시 분전반 크기를 고려하여 2배형 후 감독관의 승인을 득할 것.

NO.	DATE	REVISIONS	DRWG.	APPRV.
-----	------	-----------	-------	--------

CHANG
ARCHITECTURE
주식회사 종합건축사사무소 창

SAC INTERNATIONAL LTD.
ARCHITECTS-CONSULTANTS
서울특별시 중구 회현동 1가 11-1
주식회사 서울건축

PROJECT TITLE
전남대학교병원
제3동 진료공간 재배치 건축공사

DRAWING TITLE
지상3층 평면도

APPROVAL	이민화	PROJECT NO.	21043
CHECK	이승우	FILE NAME	A-104.DWG
DRAWING	이현지	DRAWING NO.	
SCALE	A1 : 1/60 A3 : 1/120		
DATE	2022.6.		A-104



- NOTE
- 벽체무호
BL6 : 6" 보강블럭쌓기
BR0.5 : 0.5B 시멘트벽돌쌓기
BR0.75 : 0.75B 시멘트벽돌쌓기
BR1.0 : 1.0B 시멘트벽돌쌓기
석고보드 : 석고보드 계획도와 상세도 참조
분전반 : 전기공사 전력간선 평면도 참조
 - 전남대학교 3동 리모델링 공사는 골조공사만 제외하며 범위는 지하1층~지상9층까지임. 아래 범위에 면하는 벽체를 철거하지 않는 원칙으로 하며, 평면도에 부호가 표기된 벽체만 신설 벽체임. 단, 승강기 교체는 공사범위에 포함함.
 - 계단실과 E. 홀은 "환경개선" 대상이며, 실내재료 마감표 기준으로 공사함.
 - 전남대학교병원 3동 주변의 포장 및 조경은 신설 개도파 및 실외기에 간섭되는 구간에 한해서 철거 후 재시공함.
 - 출입문, 하드웨어, 석고보드 벽체, CONC. BLOCK, 조적 벽체는 모두 건축 공사분임. 단, 벽체의 마감과 천장재, 천장틀, 바닥 마감은 인테리어 공사
 - 기존 방화구획과 그에 해당하는 벽체 공사범위 제외이며, 방화문은 재도색만 할 것
 - 승강기 교체는 본 공사에 포함함.
 - 기존 설비공간의 점검문은 손치 및 페인트 재시공 할 것.
 - 가구 : 모두 공사범위 제외임. 단, 상세도가 있는 붙박이장과 인테리어 공사에 포함된 가구는 포함함.
 - 본 공사에 엘리베이터 1대 교체 포함함
 - 소화전과 소화기는 매입형으로 설치 할 것. (A-803, 참조세도.DWG 참조 할 것.)
 - 지상1층 영상의학과 대기공간 공사범위는 확장될 수 있으며, 감독관과 협의하여 SHOP DWG 작성 후 시공할 것.
 - 샤프트 내부에는 예폭시프라이머로 6면 시공 및 오픈구간 방화실로 매물것.
 - 조화기함, 분전반의 위치는 건축도면 기준으로 시공 할 것.
 - 벽체 설치시 분전반 크기를 고려하여 2,800mm 후 감독관의 승인을 득할 것.

NO.	DATE	REVISIONS	DRWG.	APPRV.
-----	------	-----------	-------	--------

CHANG
ARCHITECTURE
주식회사 종합건축사사무소 창

SAC INTERNATIONAL LTD.
ARCHITECTS-CONSULTANTS
서울특별시 강남구 테헤란로 12-1, 12층 주식회사 서울건축

PROJECT TITLE
전남대학교병원
제3동 진료공간 재배치 건축공사

DRAWING TITLE
지상4층 평면도

APPROVAL	이민화	PROJECT NO.	21043
CHECK	이승우	FILE NAME	A-105.DWG
DRAWING	이현지	DRAWING NO.	
SCALE	A1 : 1/60 A3 : 1/120		
DATE	2022.6.		A-105

1 지상4층 평면도
축척 A1 : 1/60
A3 : 1/120



- NOTE
- 벽체번호
BL6 : 6" 보강블럭쌓기
BR0.5 : 0.5B 시멘트벽돌쌓기
BR0.75 : 0.75B 시멘트벽돌쌓기
BR1.0 : 1.0B 시멘트벽돌쌓기
석고보드 : 석고보드 계획도와 상세도 참조
분전반 : 전기공사 전력간선 평면도 참조
 - 전남대학교 3동 리모델링 공사는 골조공사를 제외하며 범위는 지하1층~지상9층까지임.
아래 범위에 면하는 벽체를 철거하지 않는 원칙으로 하며, 평면도에 부호가 표기된 벽체만 신설 벽체임.
단, 승강기 교체는 공사범위에 포함함.
= 공사범위 제외
= 환경개선범위(벽체유지, 마감재시공)
= 부분 공사범위 제외(천장만 교체)
= 인테리어 공사
 - 계단실과 EL 홀은 "환경개선" 대상이며, 실내재로 마감표 기준으로 공사항.
 - 전남대학교병원 3동 주변의 포장 및 조경은 신설 캐노피 및 실외기에 간섭되는 구간에 한해서 철거 후 재시공함.
 - 출입문, 하드웨어, 석고보드 벽체, CONC' BLOCK, 조적 벽체는 모두 건축 공사분임.
단, 벽체의 마감과 천장재, 천장틀, 바닥 마감은 인테리어 공사
 - 기존 방화구획과 그에 해당하는 벽체 공사범위 제외이며, 방화문은 재도색만 할 것
 - 승강기 교체는 본 공사에 포함함.
 - 기존 설비공간의 점검문은 존치 및 페인트 재시공 할 것.
 - 기타 모든 공사범위 제외임. 단, 상세도가 있는 붙박이장과 인테리어 공사에 포함된 가구는 포함함.
 - 본 공사에 엘리베이터 1대 교체 포함함
 - 소화전과 소화기는 매입형으로 설치 할 것. (A-603, 답상세도.DWG 참조 할 것.)
 - 지상1층 영상의학과 대기공간 공사범위는 확장될 수 있으며, 감독관과 협의하여 SHOP DWG 작성 후 시공할 것.
 - 샤프트 내부는 에폭시프라이머로 6면 시공 및 오픈구간 방화실로 메울것.
 - 조화기함, 분전반의 위치는 건축도면 기준으로 시공 할 것.
 - 벽체 설치시 분전반 크기를 고려하여 2.5배정 후 감독관의 승인을 득할 것.

NO.	DATE	REVISIONS	DRWG.	APPR.
-----	------	-----------	-------	-------


CHANG
ARCHITECTURE
주식회사 종합건축사사무소 창

SAC INTERNATIONAL LTD.
ARCHITECTS-CONSULTANTS
서울특별시 강남구 테헤란로 152 동원빌딩 11층 주식회사 서울건축

PROJECT TITLE
전남대학교병원
제3동 진료공간 재배치 건축공사

DRAWING TITLE
지상6층 평면도

APPROVAL	이민화	PROJECT NO.	21043
CHECK	이승우	FILE NAME	A-107.DWG
DRAWING	이현지	DRAWING NO.	
SCALE	A1 : 1/60 A3 : 1/120		
DATE	2022.6.		A-107

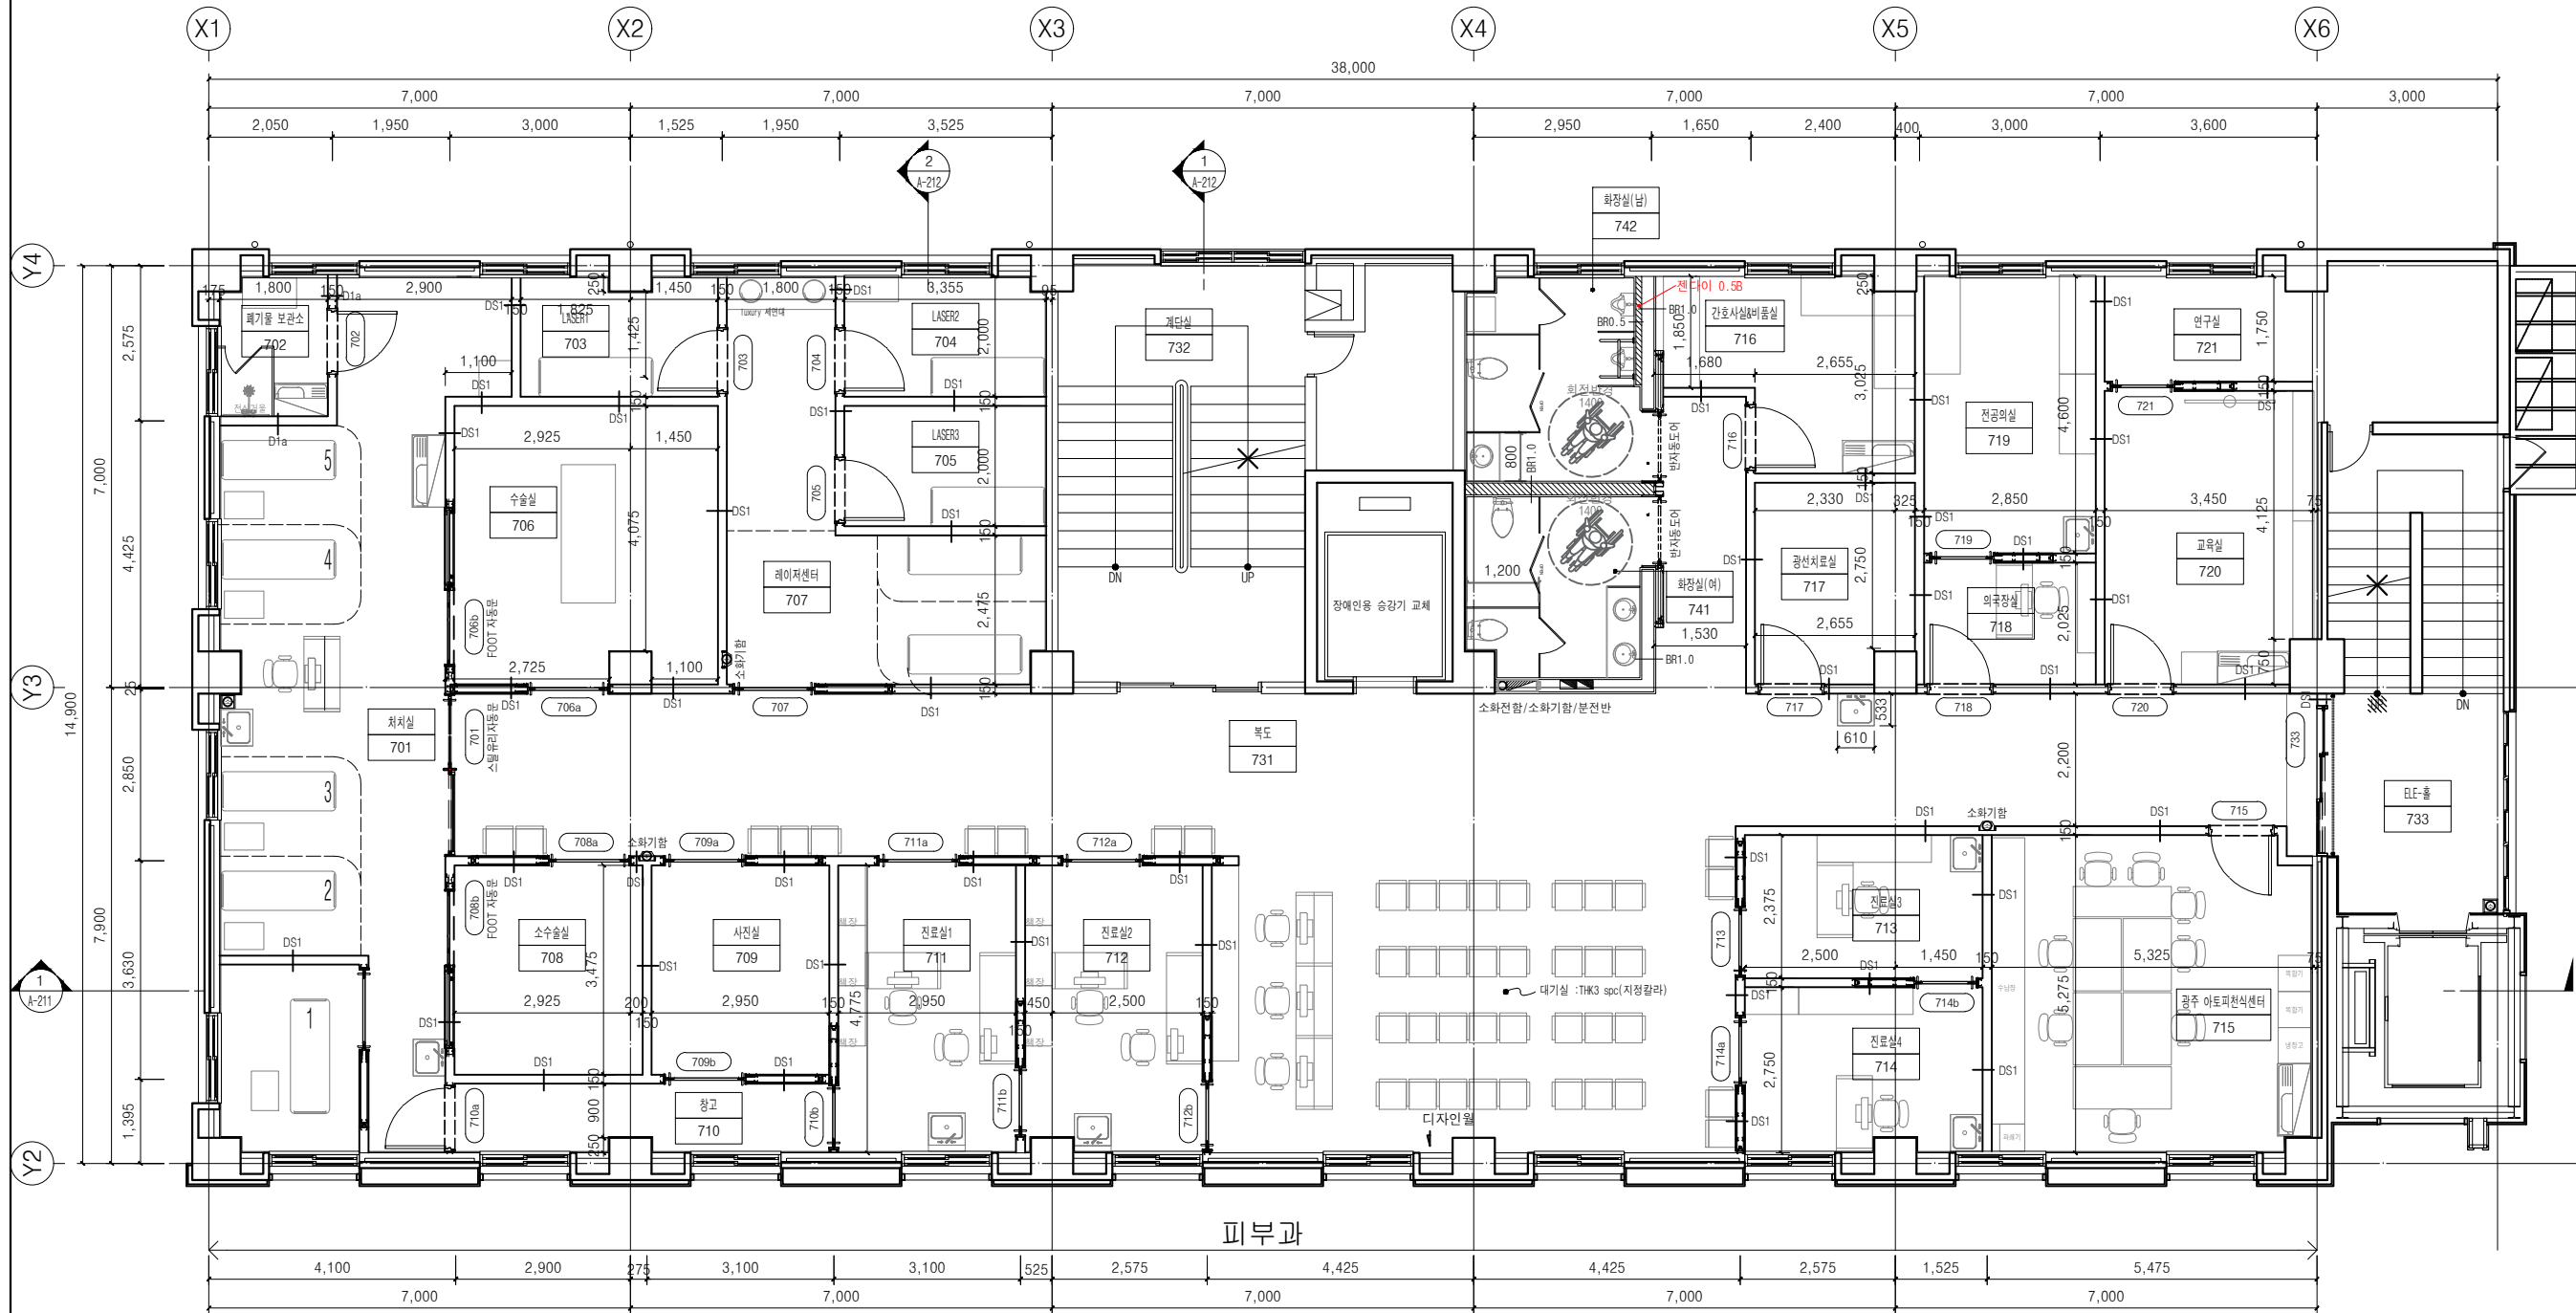

- NOTE
- 벽체무호
BL6 : 6" 보강블럭쌓기
BR0.5 : 0.5B 시멘트벽돌쌓기
BR0.75 : 0.75B 시멘트벽돌쌓기
BR1.0 : 1.0B 시멘트벽돌쌓기
석고보드 : 석고보드 계획도와 상세도 참조
■ 분전반: 전기공사 전력간선 평면도 참조
 - 전남대학교 3동 리모델링 공사는 골조공사로 제외하며 범위는 지하1층~지상9층까지임. 아래 범위에 연하는 벽체를 철거하지 않는 원칙으로 하며, 평면도에 무호가 표기된 벽체만 신설 벽체임.
단, 승강기 교체는 공사범위에 포함함.
■ = 공사범위 제외
■ = 환경개선범위(벽체유지, 마감재시공)
■ = 부분 공사범위 제외(천장만 교체)
■ = 인테리어 공사
 - 계단실과 EL 홀은 "환경개선" 대상이며, 실내재로 마감표 기준으로 공사함.
 - 전남대학교병원 3동 주변의 포장 및 조경은 신설 개도파 및 실외기에 간섭되는 구간에 광해설 철거 후 재시공함.
 - 충합문, 하드웨어, 석고보드 벽체, CONC BLOCK, 조적 벽체는 모두 건축 공사분임. 단, 벽체의 마감과 천장재, 천장등, 바닥 마감은 인테리어 공사
 - 기존 방화구획과 그에 해당하는 벽체 공사범위 제외이며, 방화문은 재도색만 할 것
 - 승강기 교체는 본 공사에 포함함.
 - 기존 설비공간의 점검문은 존치 및 페인트 재시공 할 것.
 - 기타 모든 공사범위 제외임. 단, 상세도가 있는 붙박이장과 인테리어 공사에 포함된 판구는 포함함.
 - 본 공사에 엘리베이터 1대 교체 포함함
 - 조화전과 소화기는 매입형으로 설치 할 것. (A-803, 답상세도.DWG 참조 할 것.)
 - 지상1층 영상의학과 대기공간 공사범위는 확장될 수 있으며, 감독관과 협의하여 SHOP DWG 작성 후 시공할 것.
 - 샤프트 내부에는 예폭프라이머로 6면 시공 및 오픈구간 방화실로 메울것.
 - 조화기함, 분전반의 위치는 건축도면 기준으로 시공 할 것.
 - 벽체 설치시 분전반 크기를 고려하여 2.55m형 후 감독관의 승인을 득할 것.

1 지상7층 평면도
축척 A1 : 1/60 A3 : 1/120

NO.	DATE	REVISIONS	DRWG.	APPR.
CHANG ARCHITECTURE 주식회사 종합건축사사무소 창				
SAC INTERNATIONAL LTD. ARCHITECTS-CONSULTANTS 서울특별시 강남구 테헤란로 12-1 11층 주식회사 서울건축				
PROJECT TITLE 전남대학교병원 제3동 진료공간 재배치 건축공사				
DRAWING TITLE 지상7층 평면도				
APPROVAL	이민화	PROJECT NO.	21043	
CHECK	이승우	FILE NAME	A-108.DWG	
DRAWING	이현지	A-108.DWG		
SCALE	A1: 1/60 A3: 1/120	DRAWING NO.		
DATE	2022.6.	A-108		