



제7동

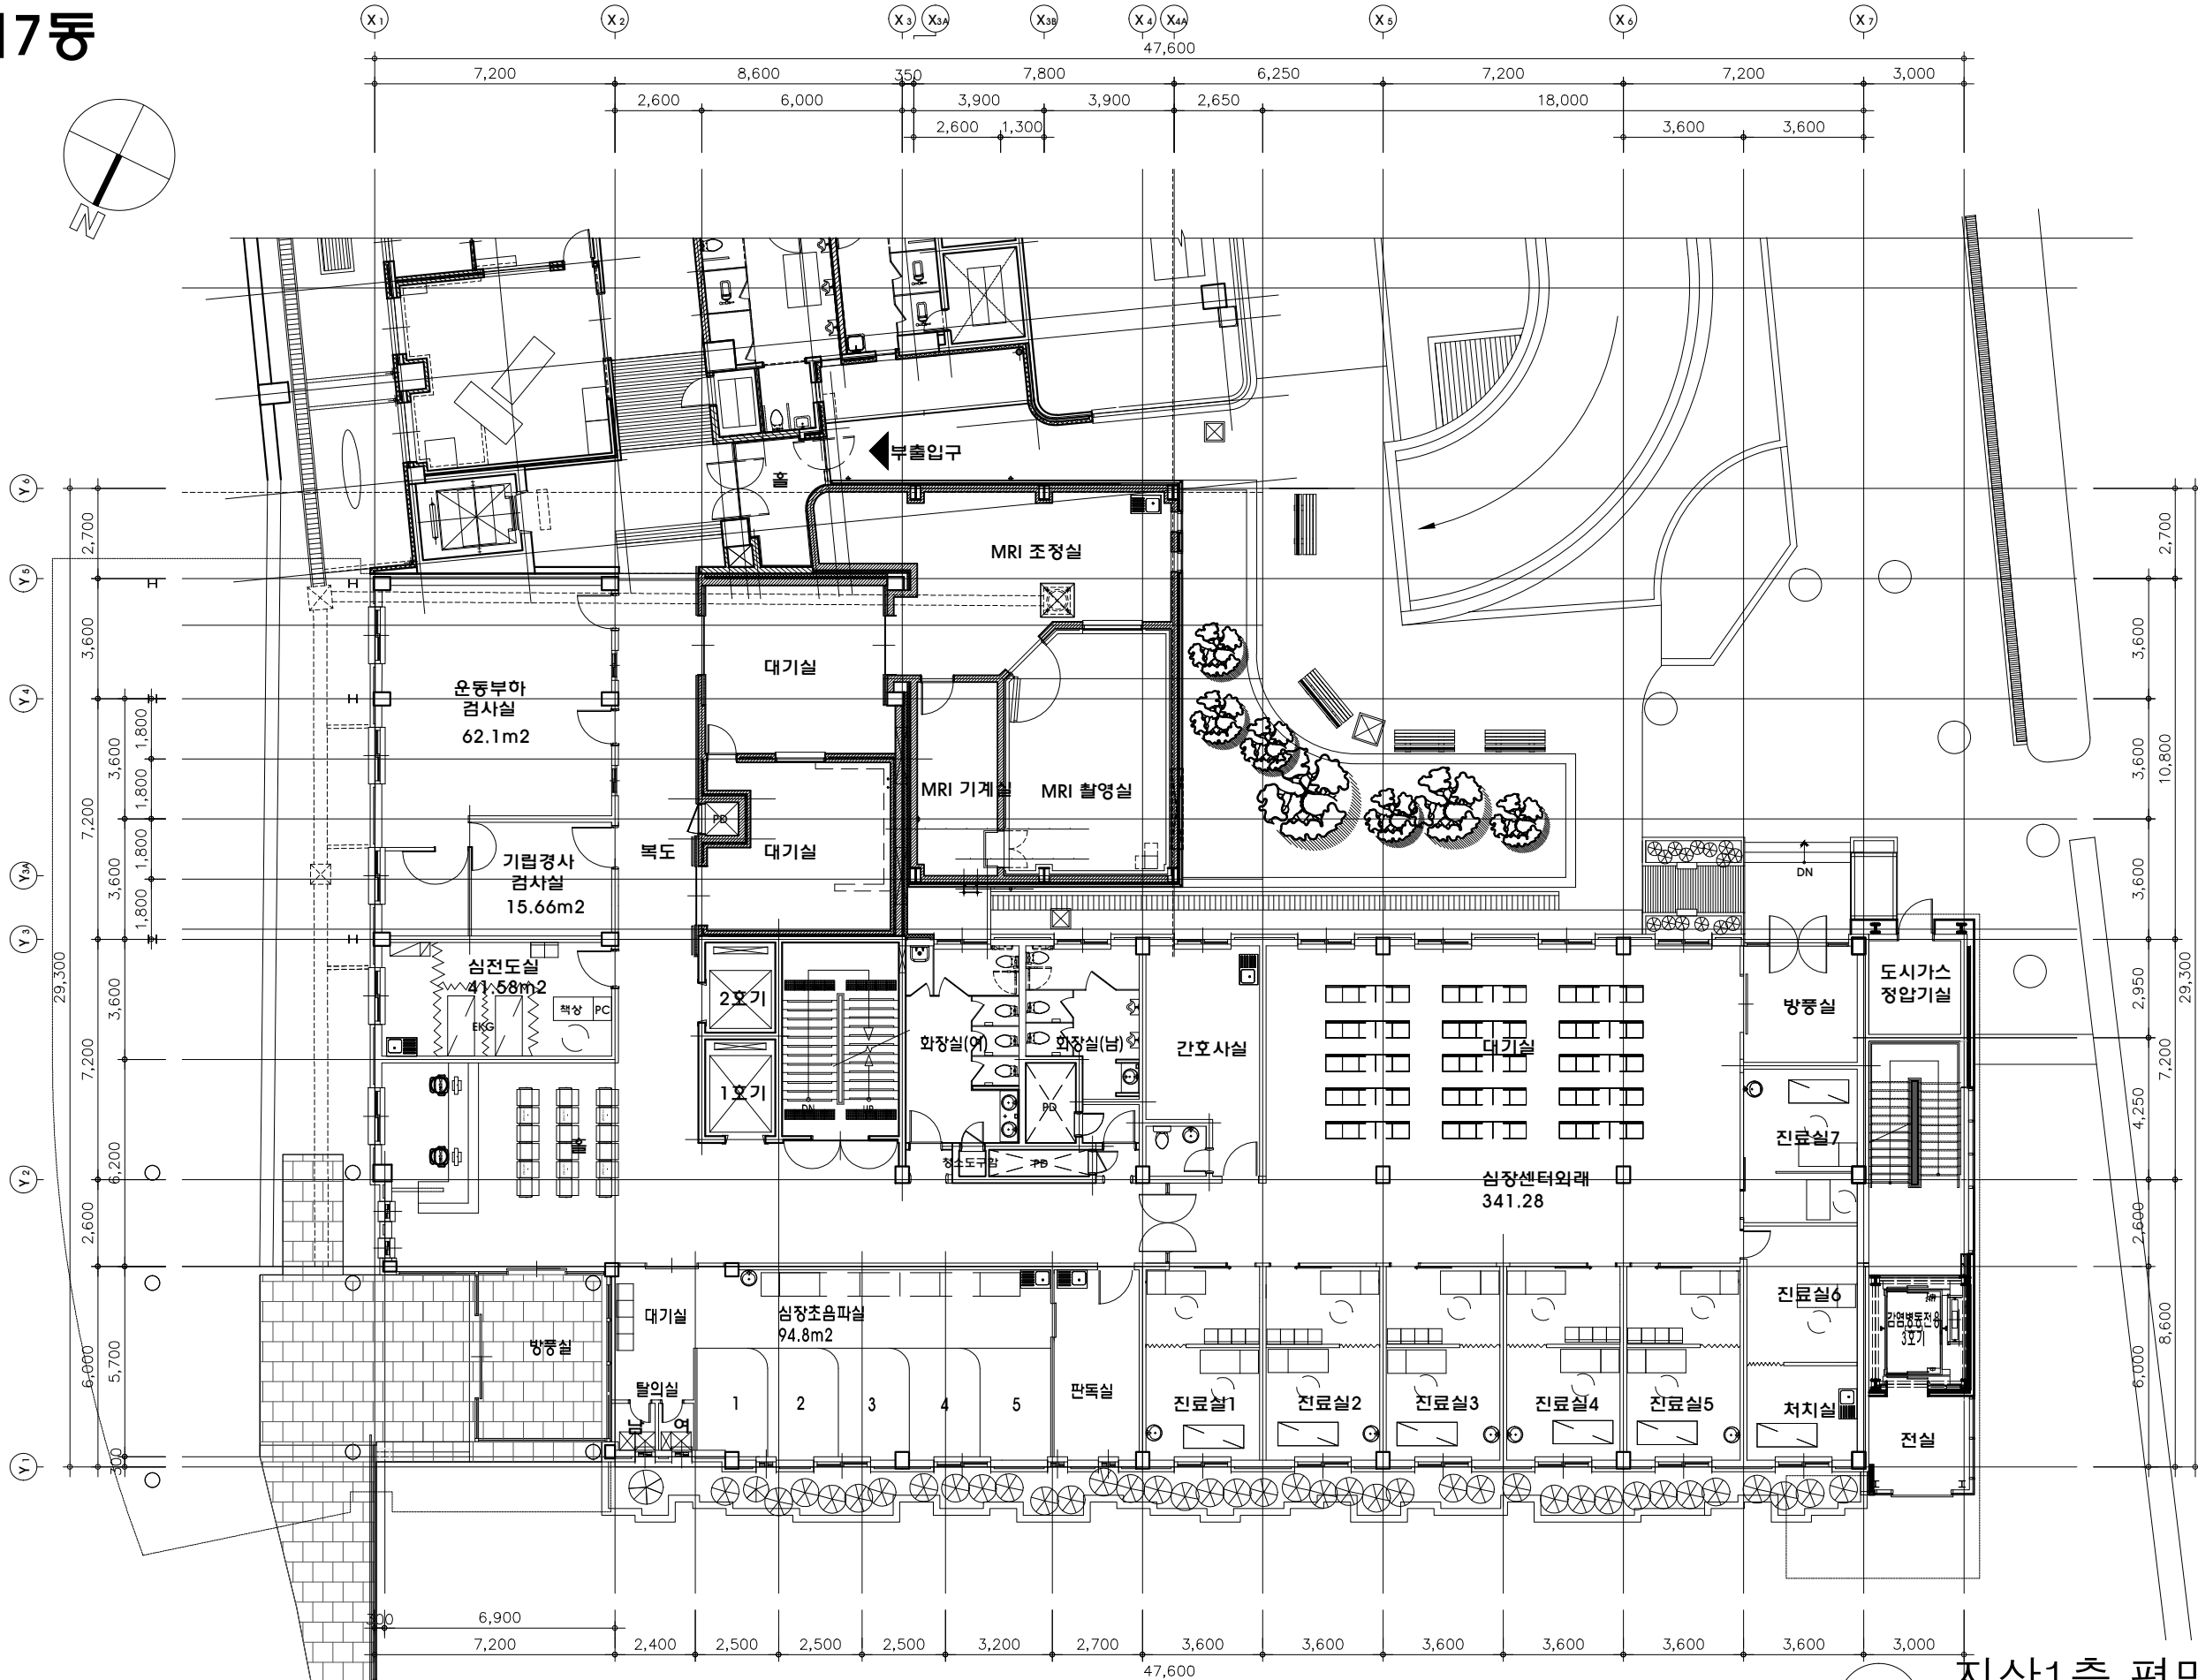

지상1층 평면도
 축척 : 1/100(A1), 1/200(A3)
 면적 : 985.65m²

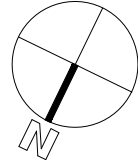

전남대학교병원
CHONNAM UNIVERSITY HOSPITAL

설계명 PROJECT TITLE

설 계

검 토

책임기술자

특기사항 NOTE

설계명 DESCRIPTION OF REV.	일자 DATE	작성 DRAW	검토 CHECK	승인 APPR

합 의

도면명 DRAWING TITLE

제7동 1층 평면도

일 자 DATE 축 척 SCALE

2018 06 A1 : 1/100
A3 : 1/200

와 일 명 FILE NAME

도면번호 DRAWING NO.

A 0 7 - 0 0 2

일련번호 SHEET NO.

□□□□-□□□□

제7동



전남대학교병원
CHONNAM UNIVERSITY HOSPITAL

설계명 PROJECT TITLE

설 계

검 토

책임기술자

특기사항 NOTE

설계변경 DESCRIPTION OF REV.	일자 DATE	작성 DRAW	검토 CHECK	승인 APPR

합 의

도면명 DRAWING TITLE

제7동 2층 평면도

일 자 DATE	축 척 SCALE
2018 06	A1 : 1/100 A3 : 1/200

와 일 명 FILE NAME

도면번호 DRAWING NO.

A 0 7 - 0 0 3

일련번호 SHEET NO.

□□□□-□□□□□



1 지상2층 평면도
축척 : 1/100(A1), 1/200(A3)
면적 : 1,301.78㎡