

제8동



제8동 1층 평면도(변경후)
S= 1 / 150(A1), 300(A3)
면적= 1,861.91m²



전남대학교병원
CHONNAM UNIVERSITY HOSPITAL

설계명 PROJECT TITLE

설 계

검 토

책임기술자

특기사항 NOTE

설계변경 DESCRIPTION OF REV.	일 자 DATE	작성 DRAW	검 토 CHECK	승 인 APPR
--------------------------------	-------------	------------	--------------	-------------

도 면 명 DAWING TITLE

제8동 1층 평면도

일 자 DATE	척 SCALE
-------------	------------

2017 05	A1 : 1/150 A3 : 1/300
---------	--------------------------

와 일 명 FILE NAME


도면번호 DRAWING NO.

A 0 8 - 0 0 4

일련번호 SHEET NO.

□□□□-□□□□

제8동

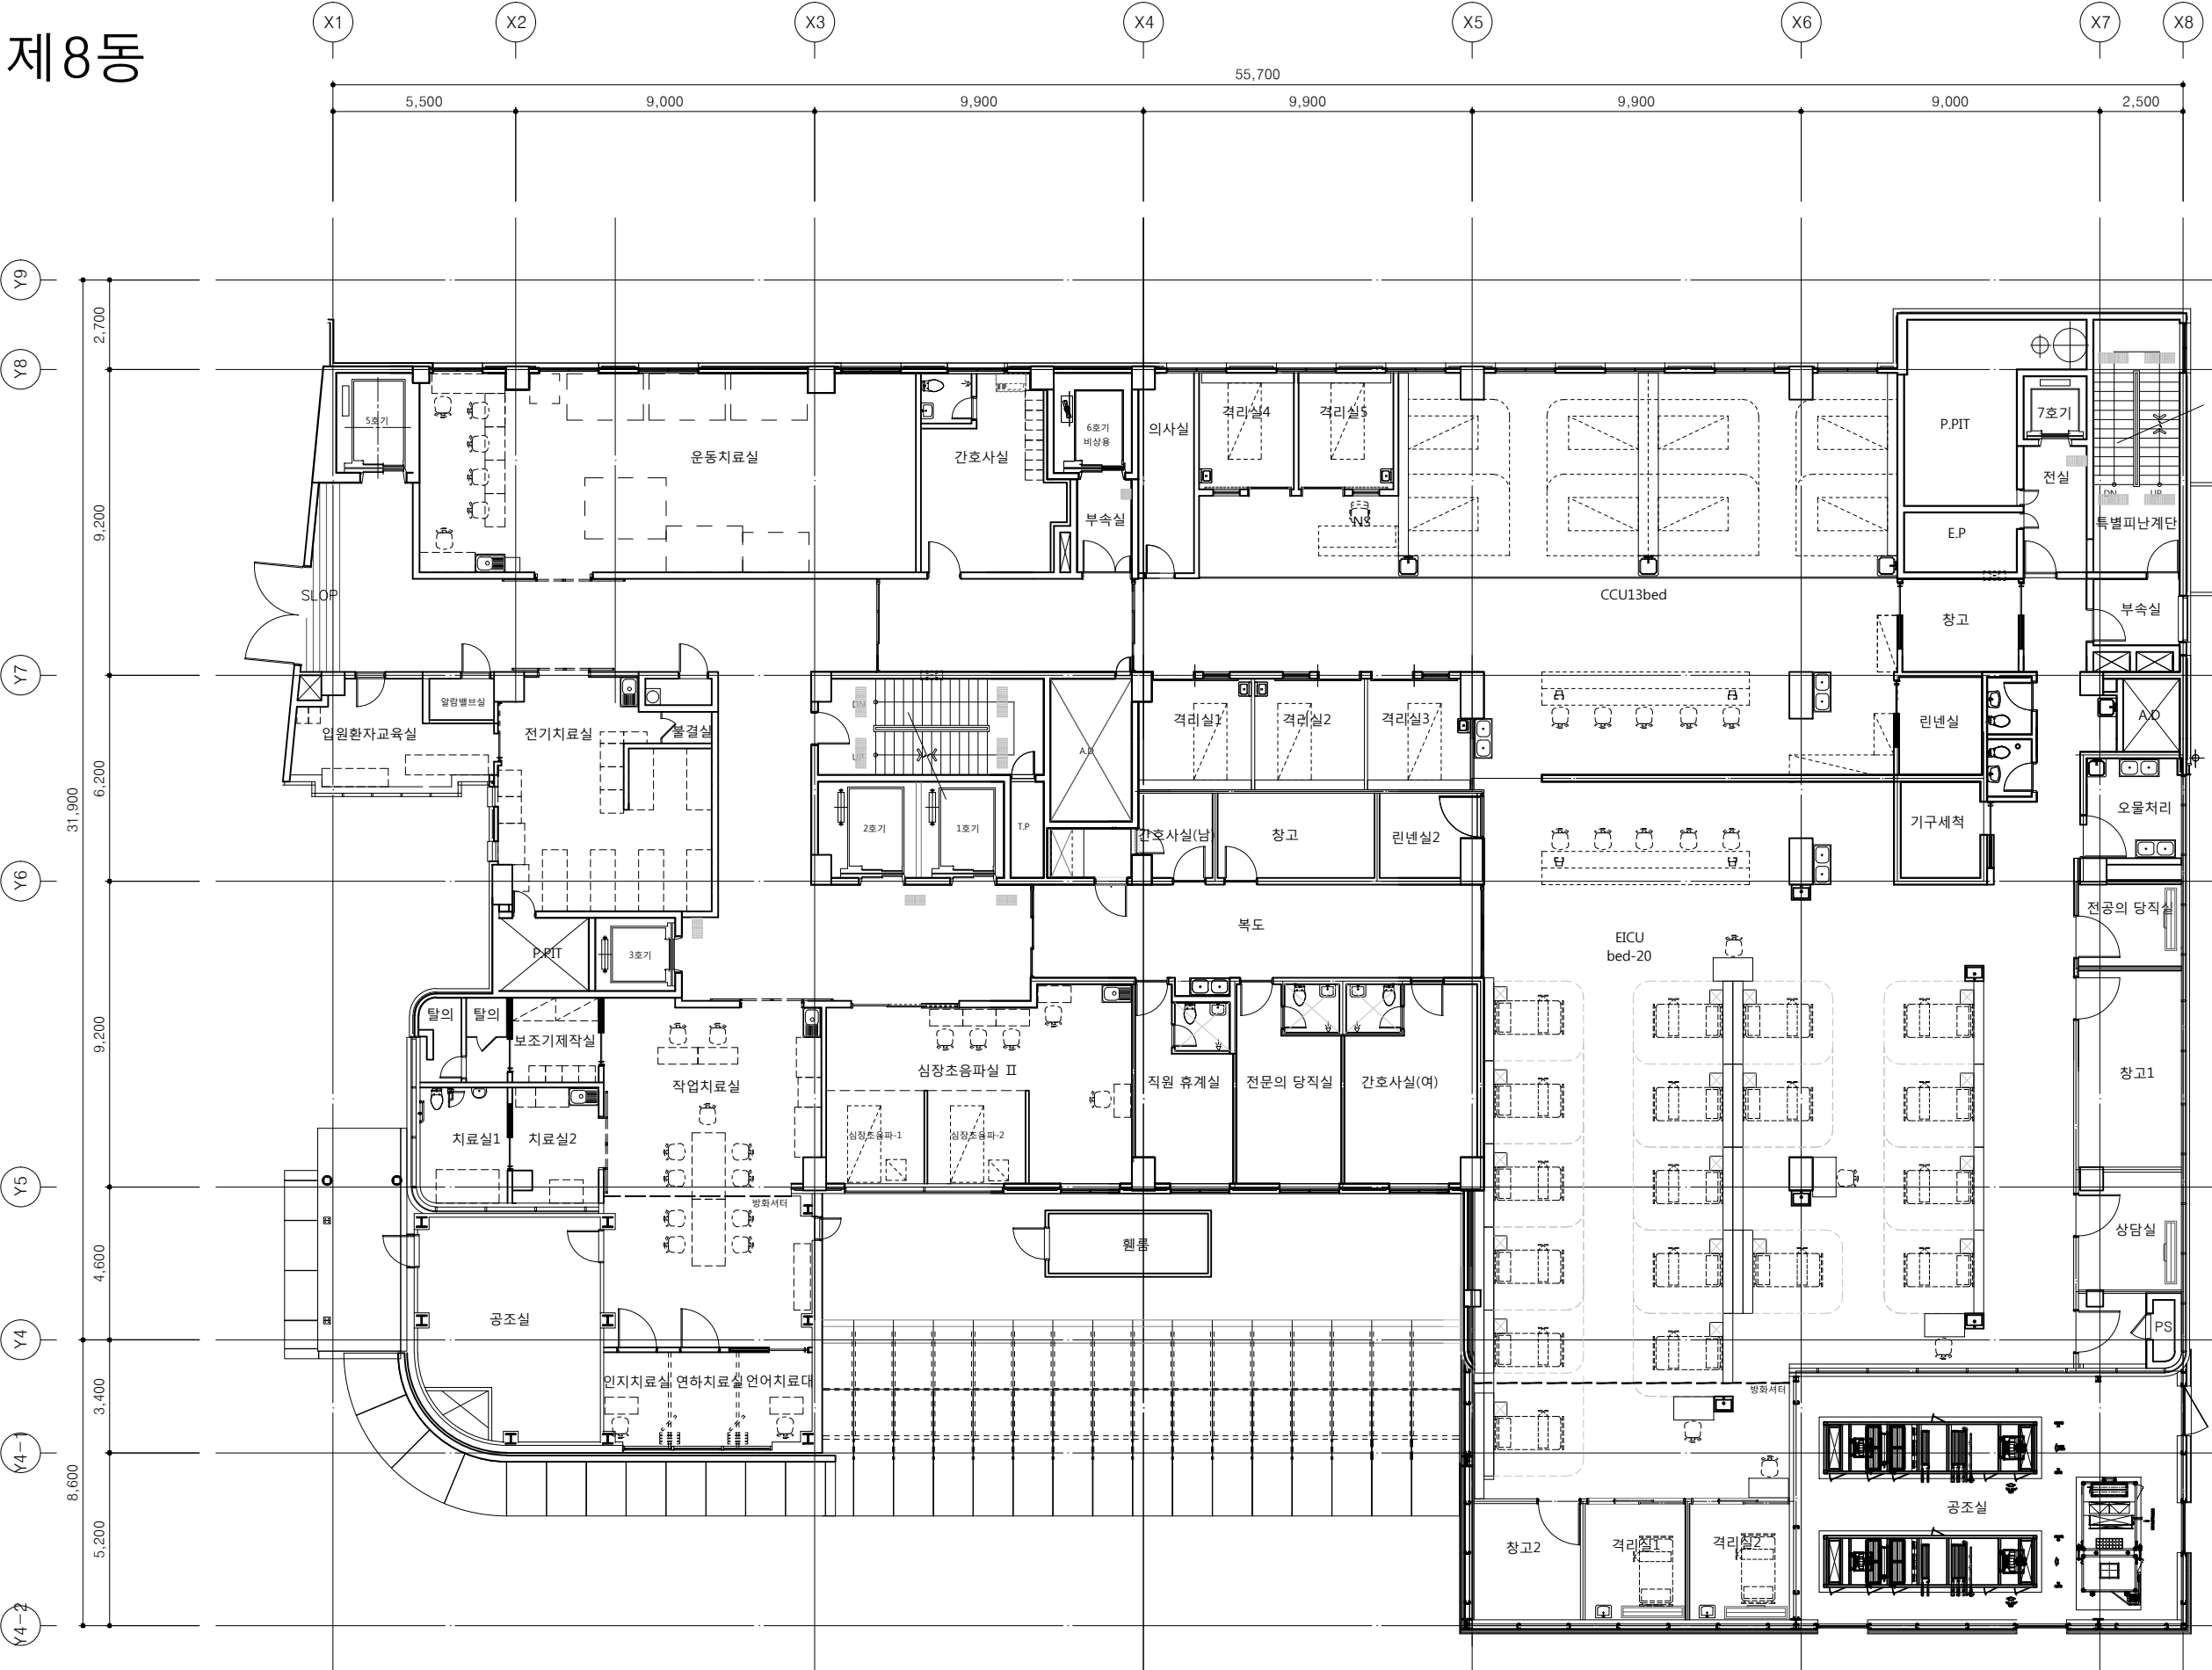

2층 평면도
축척 : 1/100A1, 1/200A3
면적=1,719.73m2



전남대학교병원
CHONNAM UNIVERSITY HOSPITAL

설계명 PROJECT TITLE

설 계

검 토

책임기술자

특기사항 NOTE

설계변경 DESCRIPTION OF REV.	일자 DATE	작성 DRAW	검토 CHECK	승인 APPR
--------------------------------	------------	------------	-------------	------------

협 의

도면명 DRAWING TITLE

제8동 2층 평면도

일자 DATE 축척 SCALE

2015 02 A1 : 1/100
A3 : 1/200

파일명 FILE NAME

도면번호 DRAWING NO.

A 0 8 - 0 0 5

일련번호 SHEET NO.

□□□□-□□□□□□